


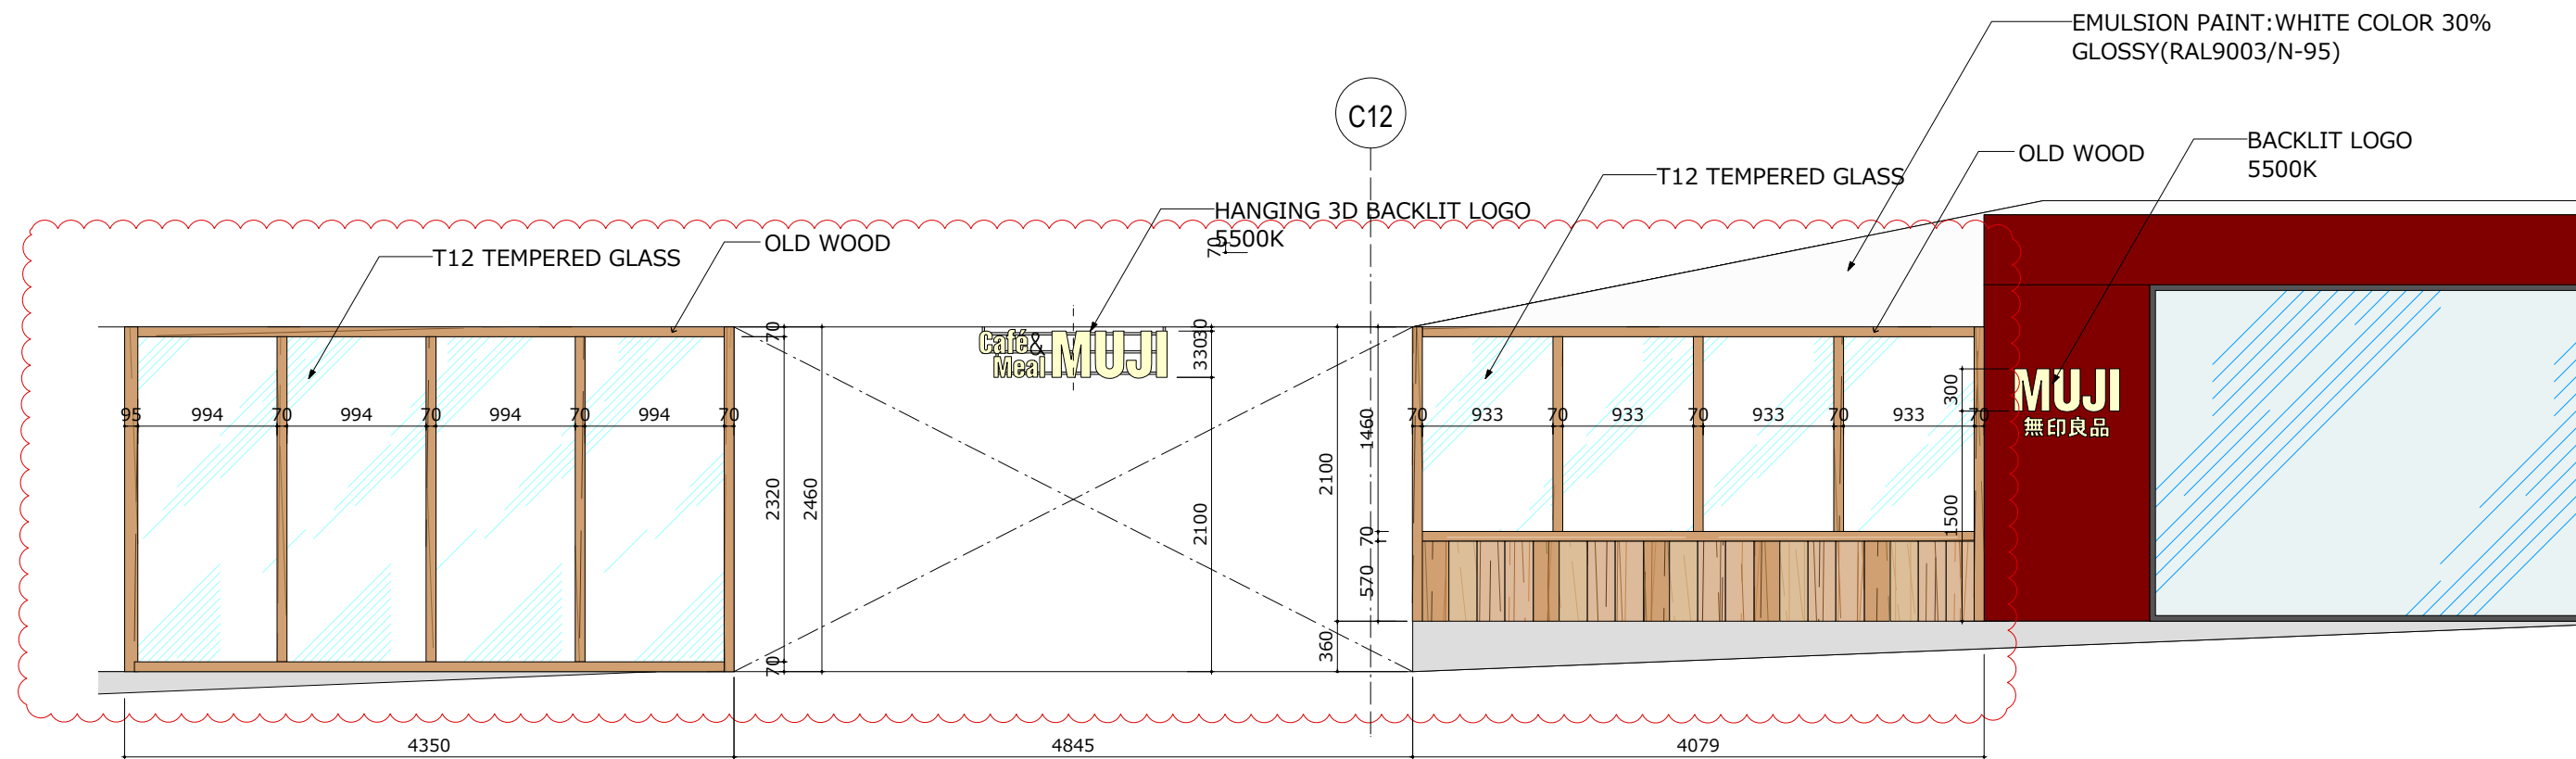


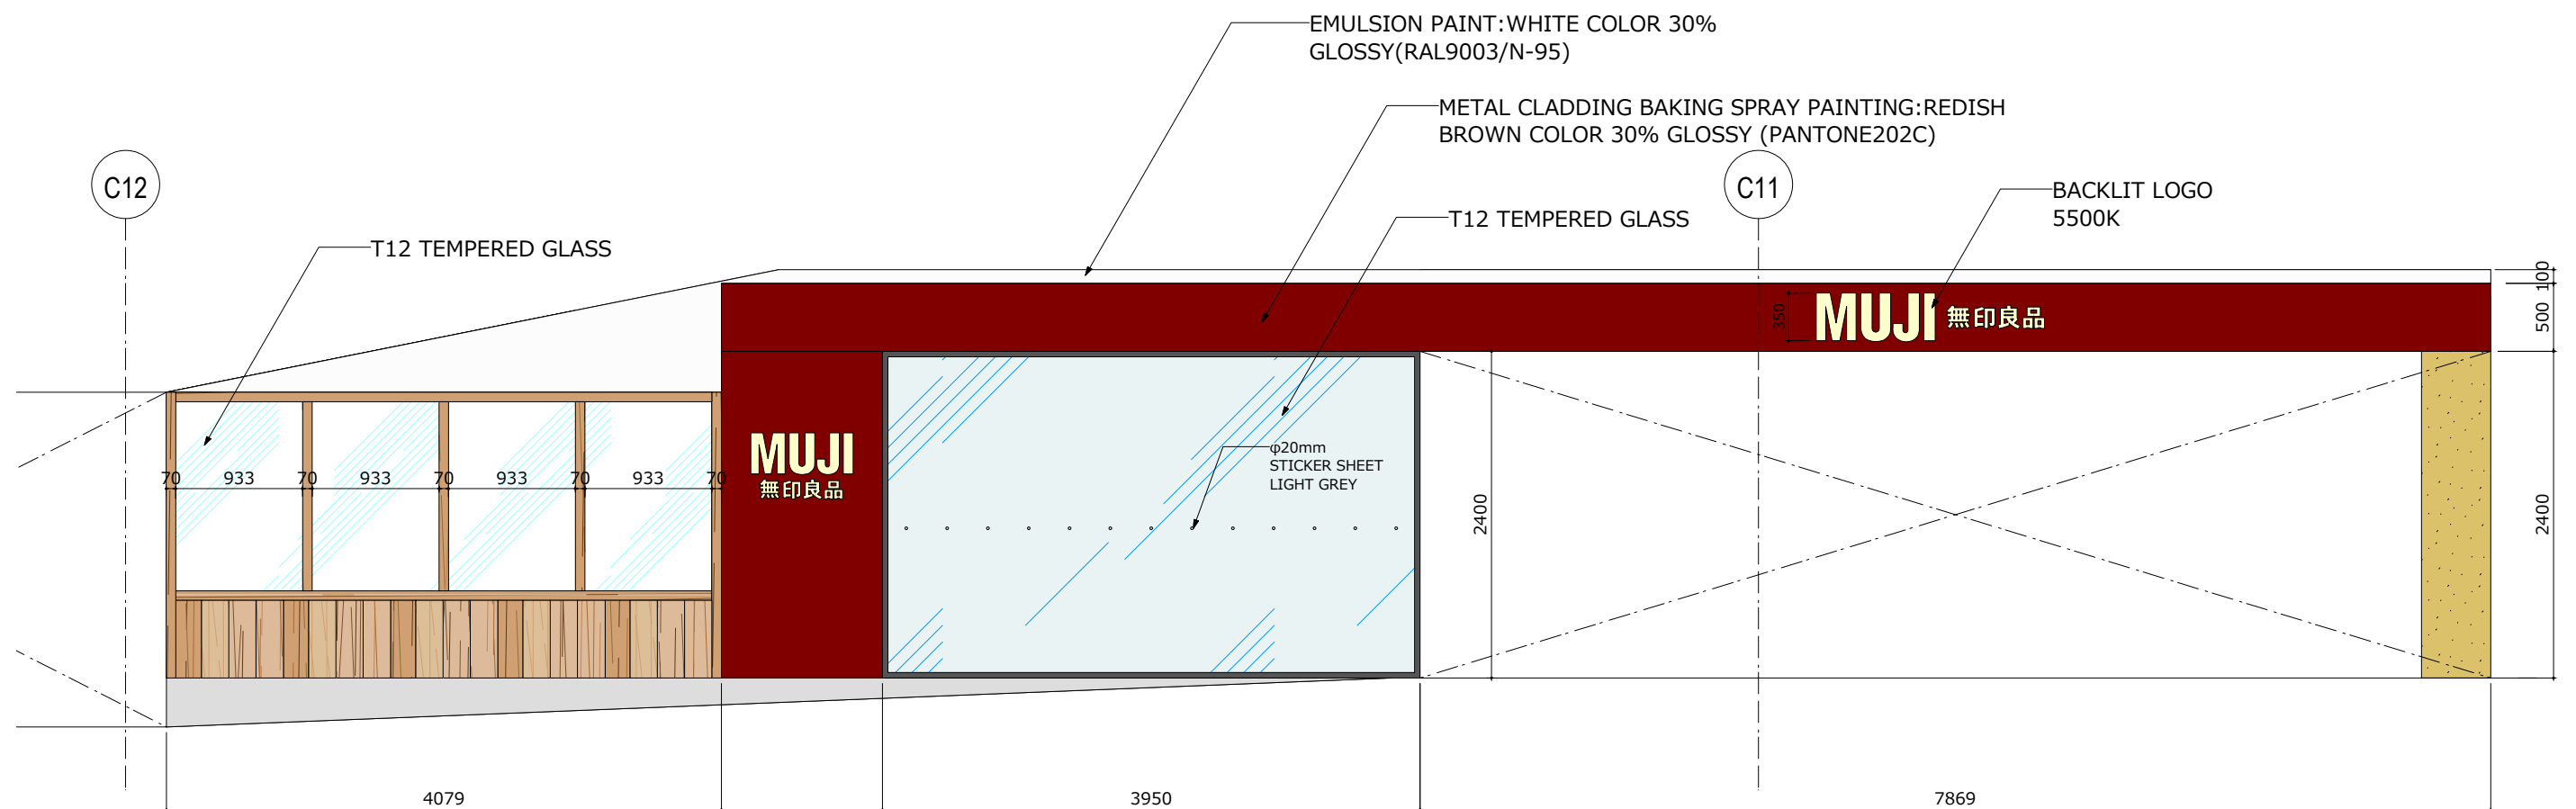


1 ELEVATION
1:50

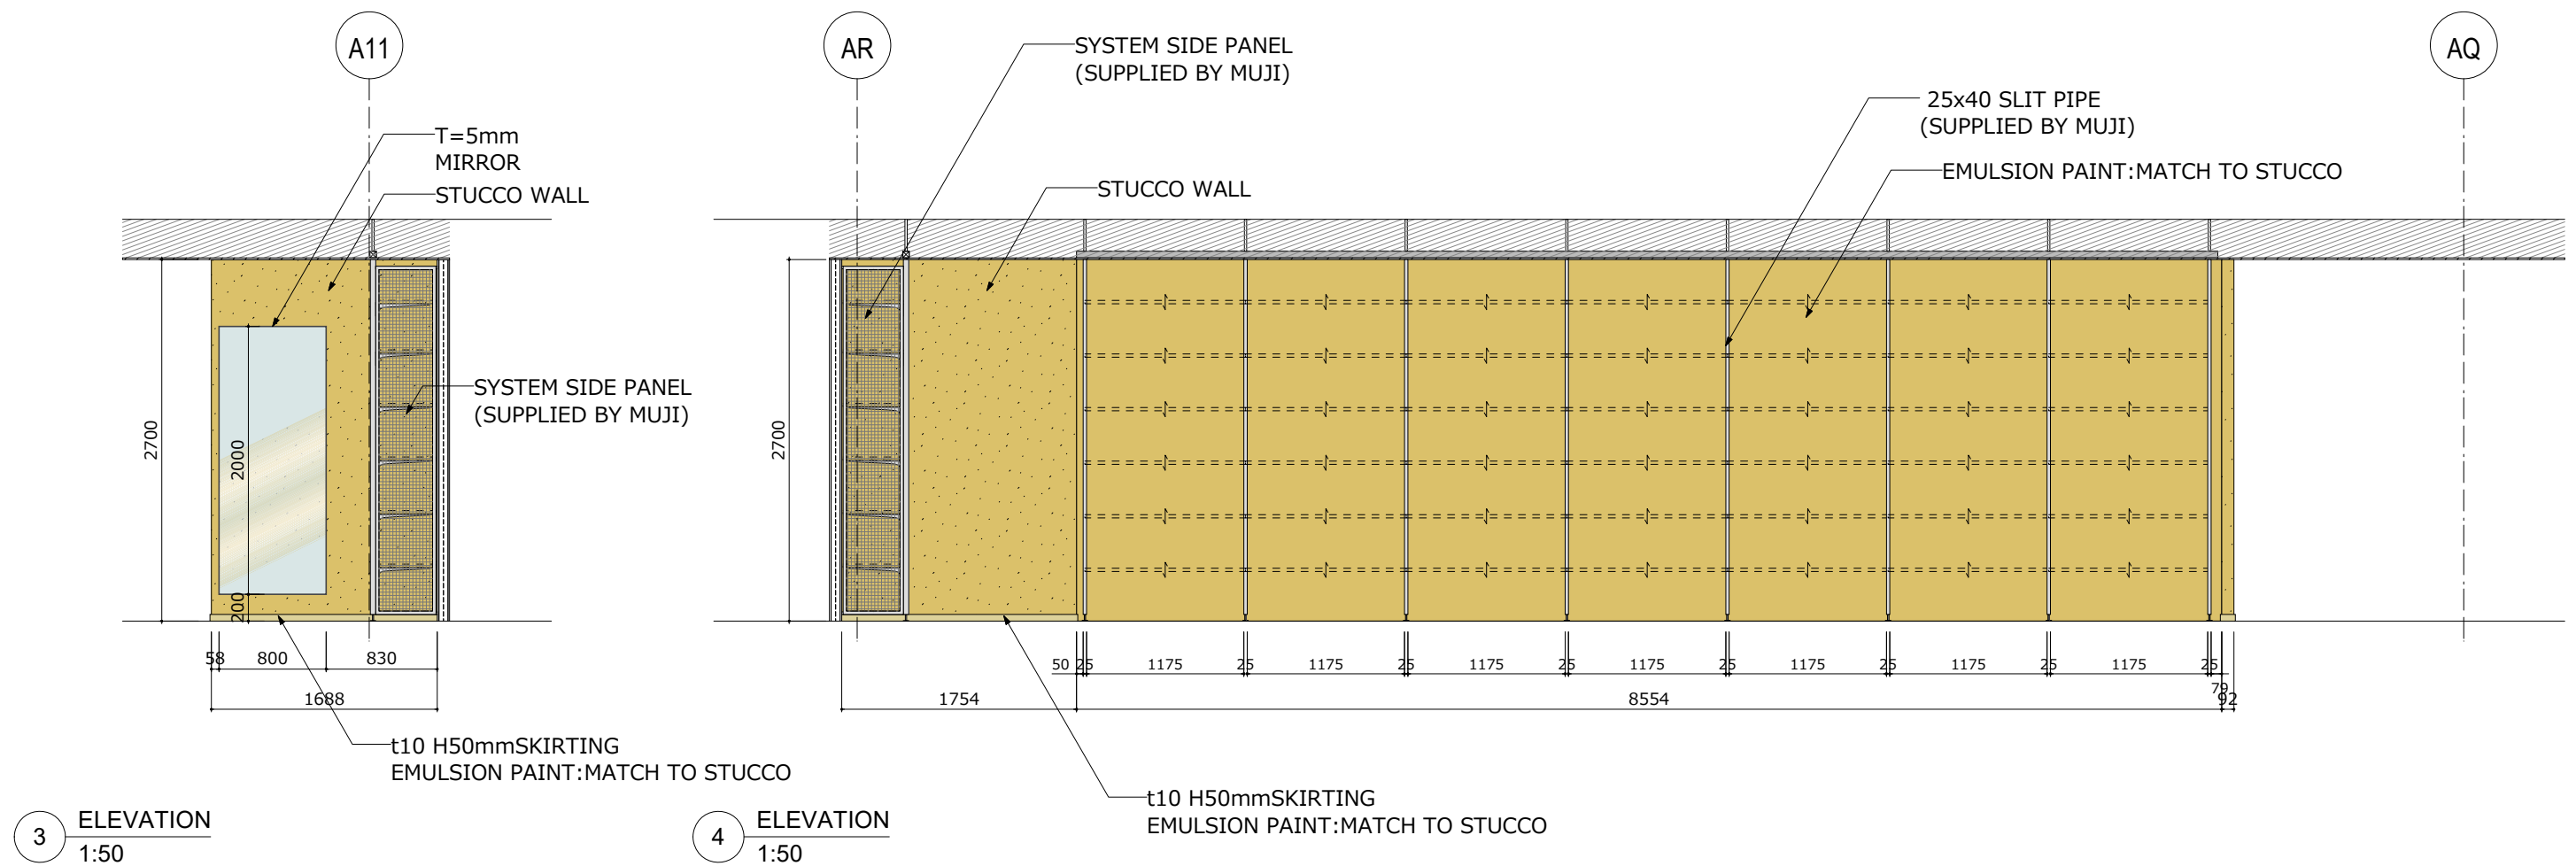


1 ELEVATION
1:50

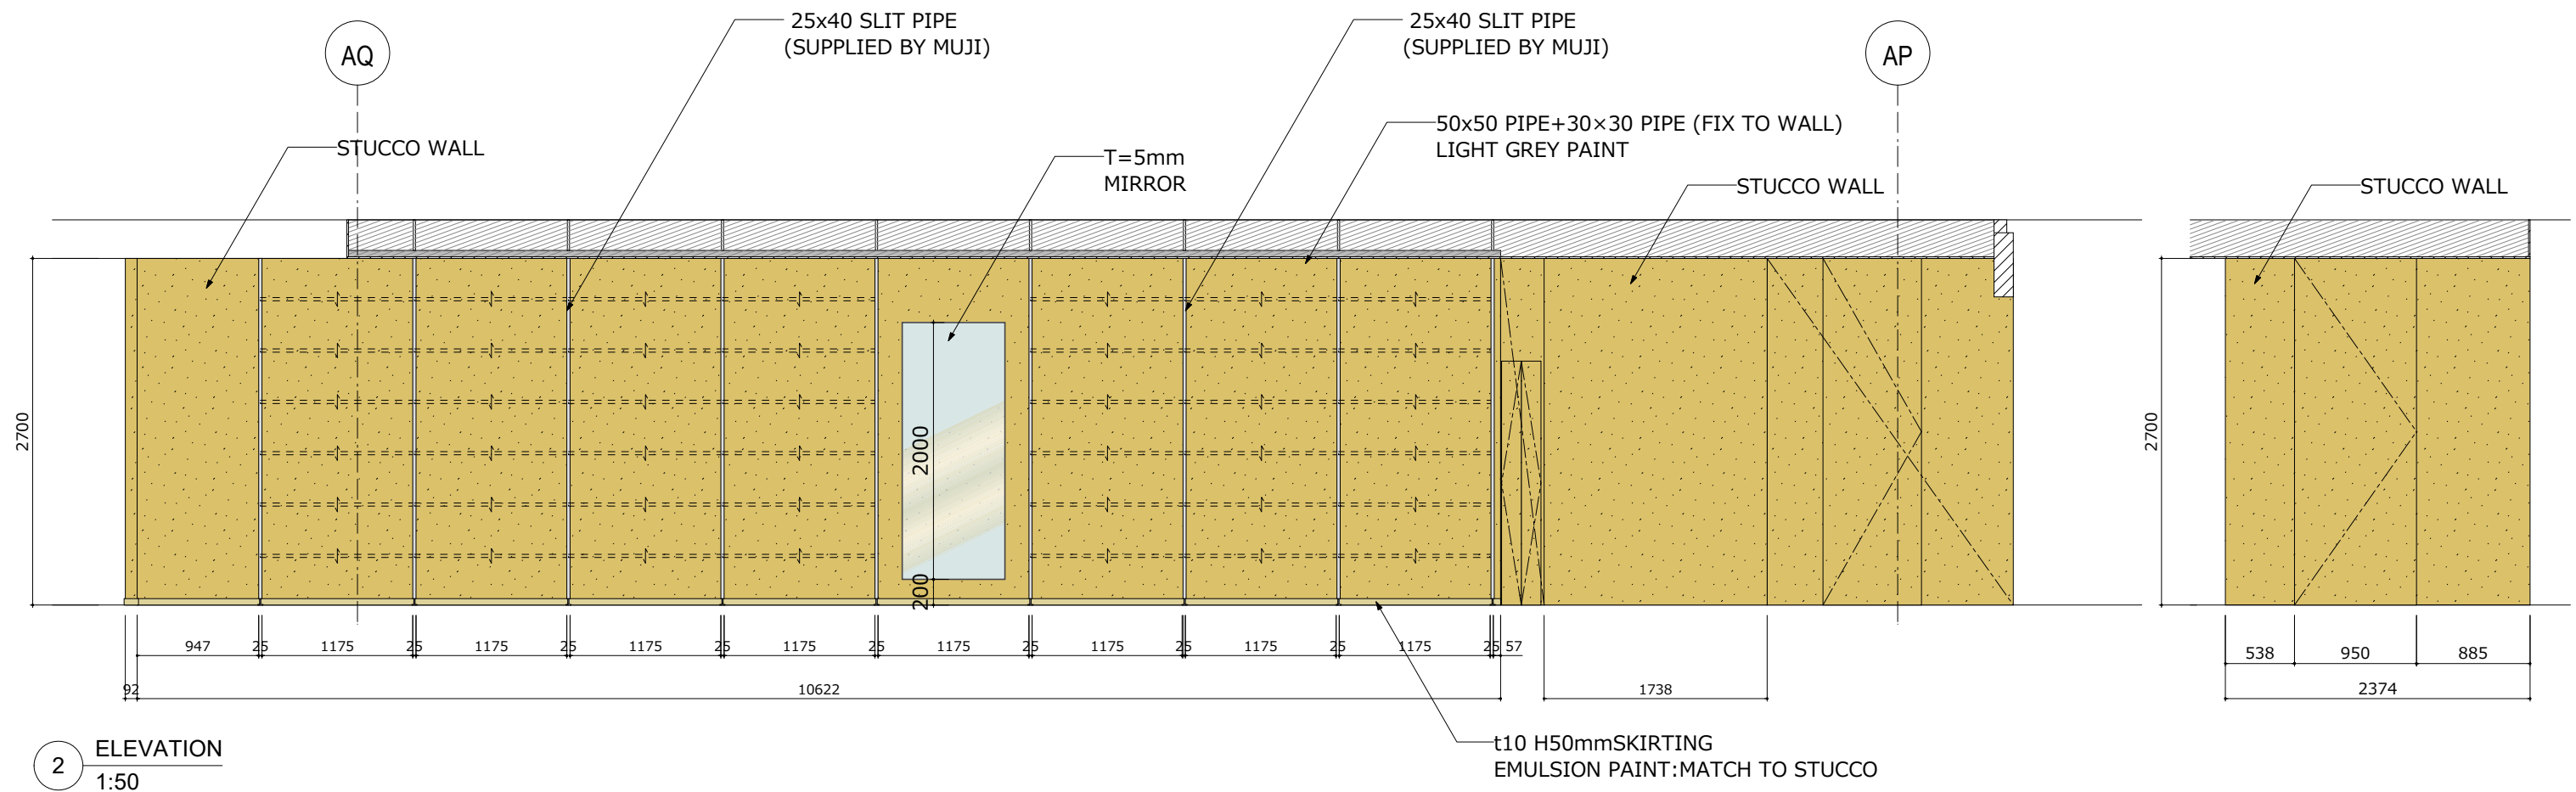

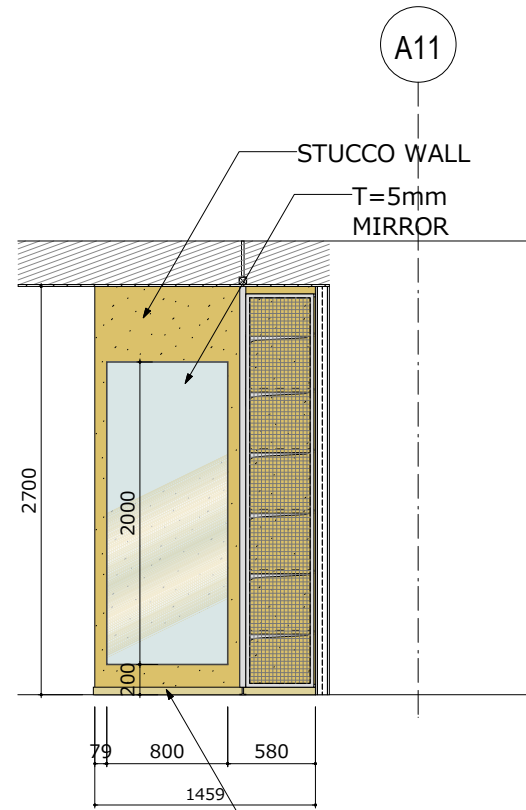


5 ELEVATION
1:50

t10 H50mm SKIRTING
EMULSION PAINT: MATCH TO STUCCO

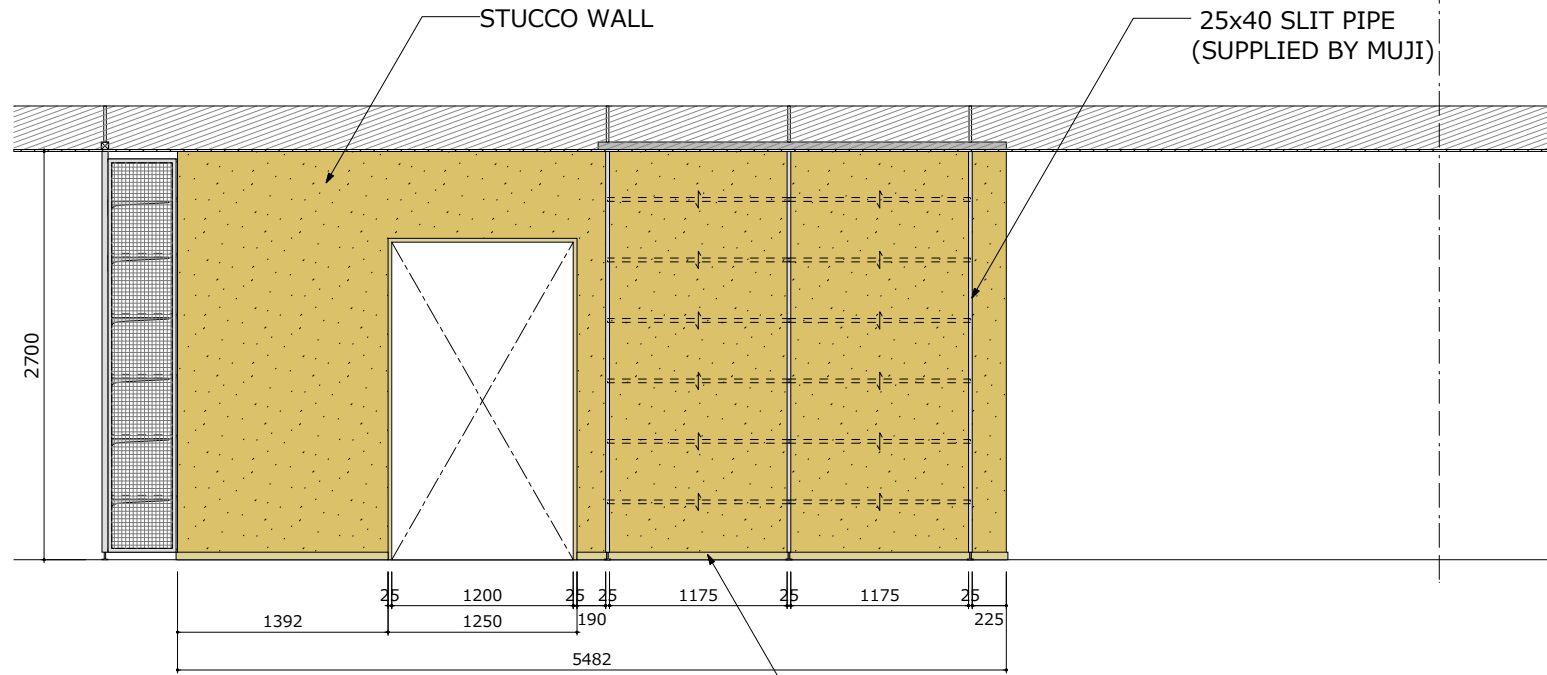


6 ELEVATION
1:50

t10 H50mm SKIRTING
EMULSION PAINT: MATCH TO STUCCO

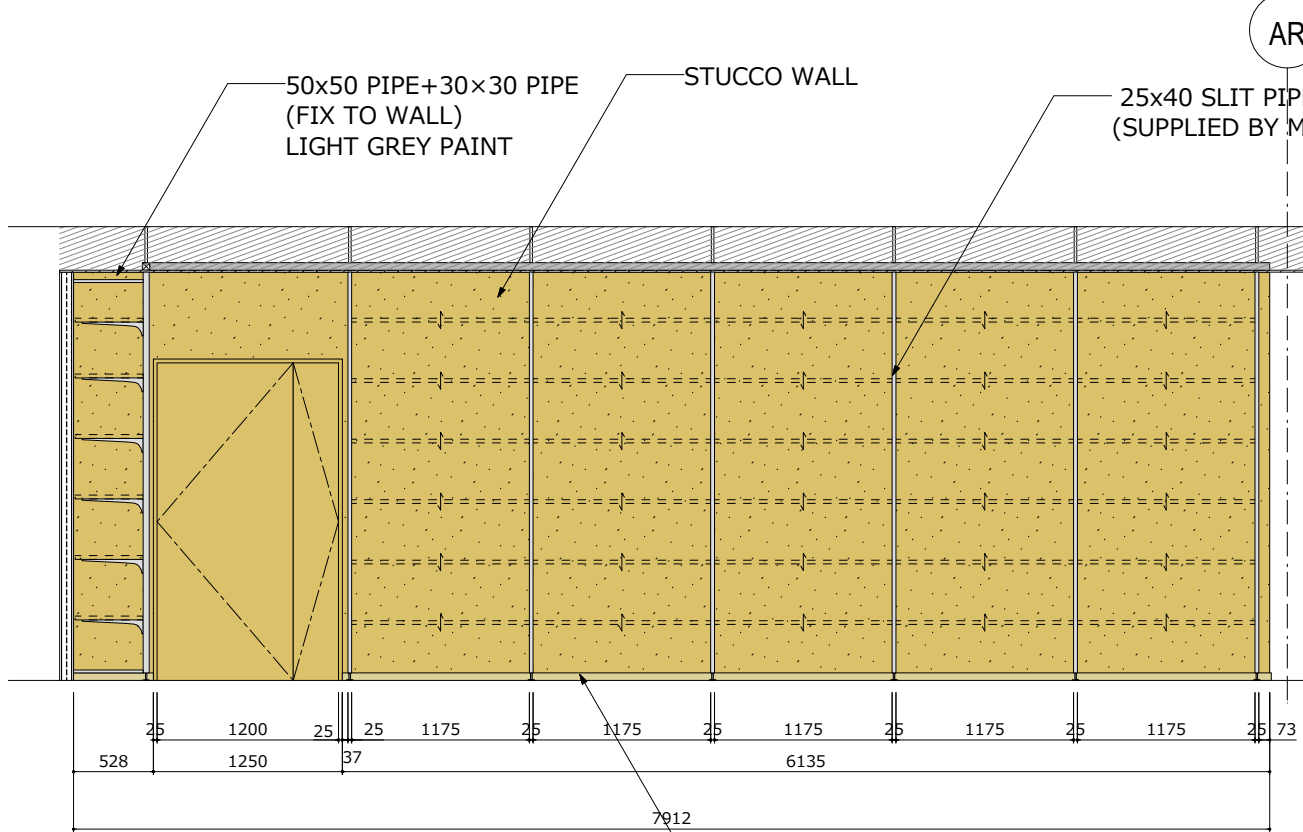



7 ELEVATION
1:50


t10 H50mm SKIRTING
EMULSION PAINT: MATCH TO STUCCO

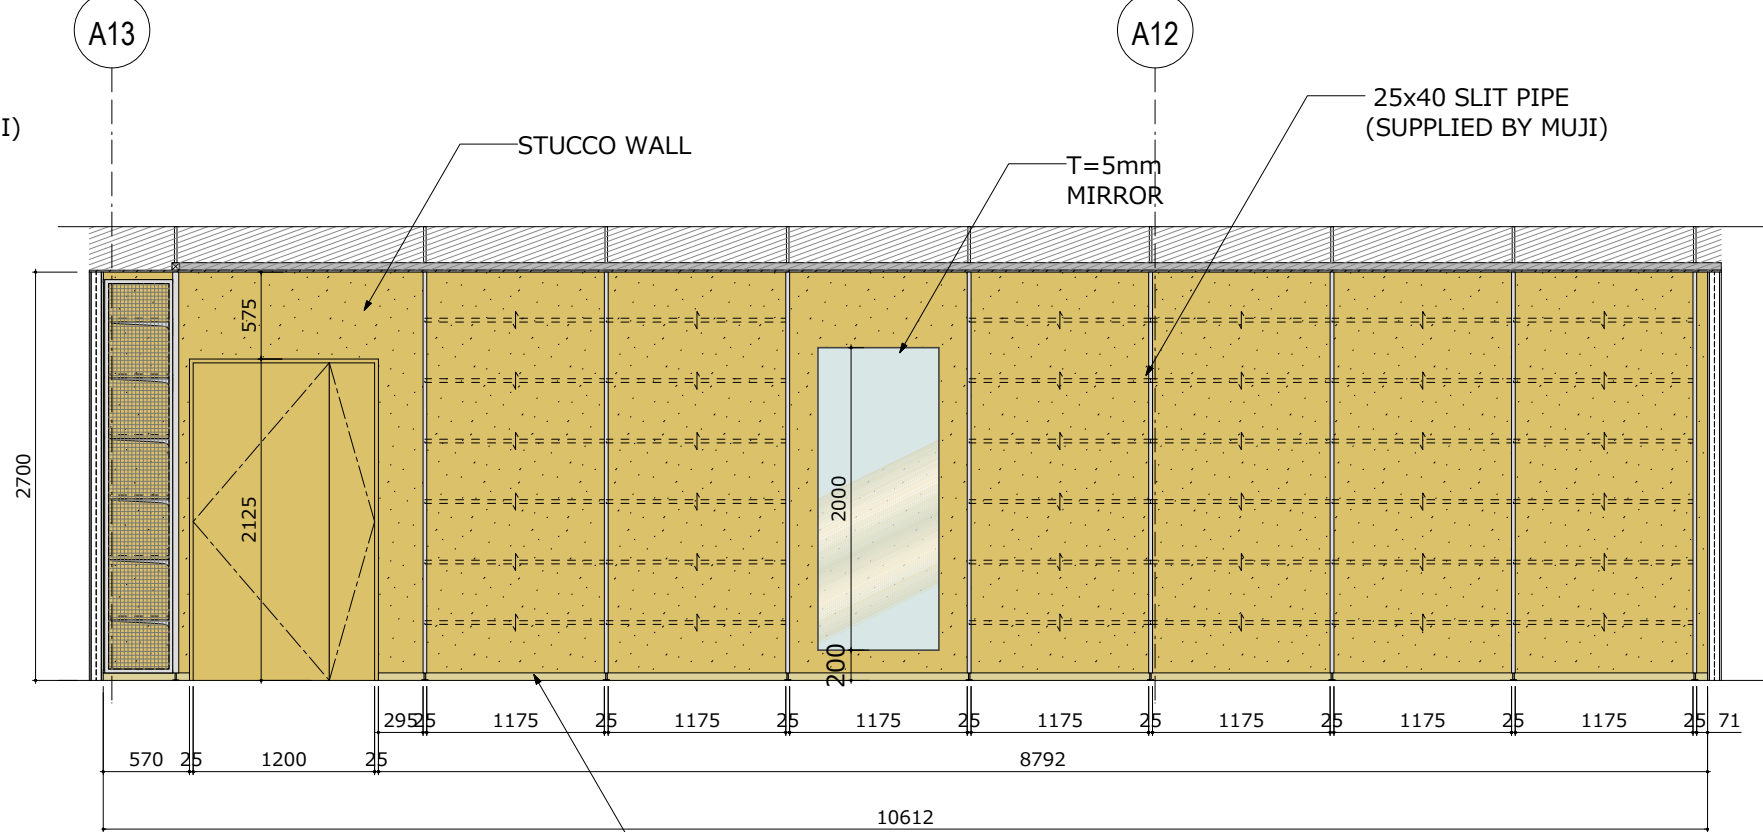


8 ELEVATION
1:50

t10 H50mm SKIRTING
EMULSION PAINT: MATCH TO STUCCO

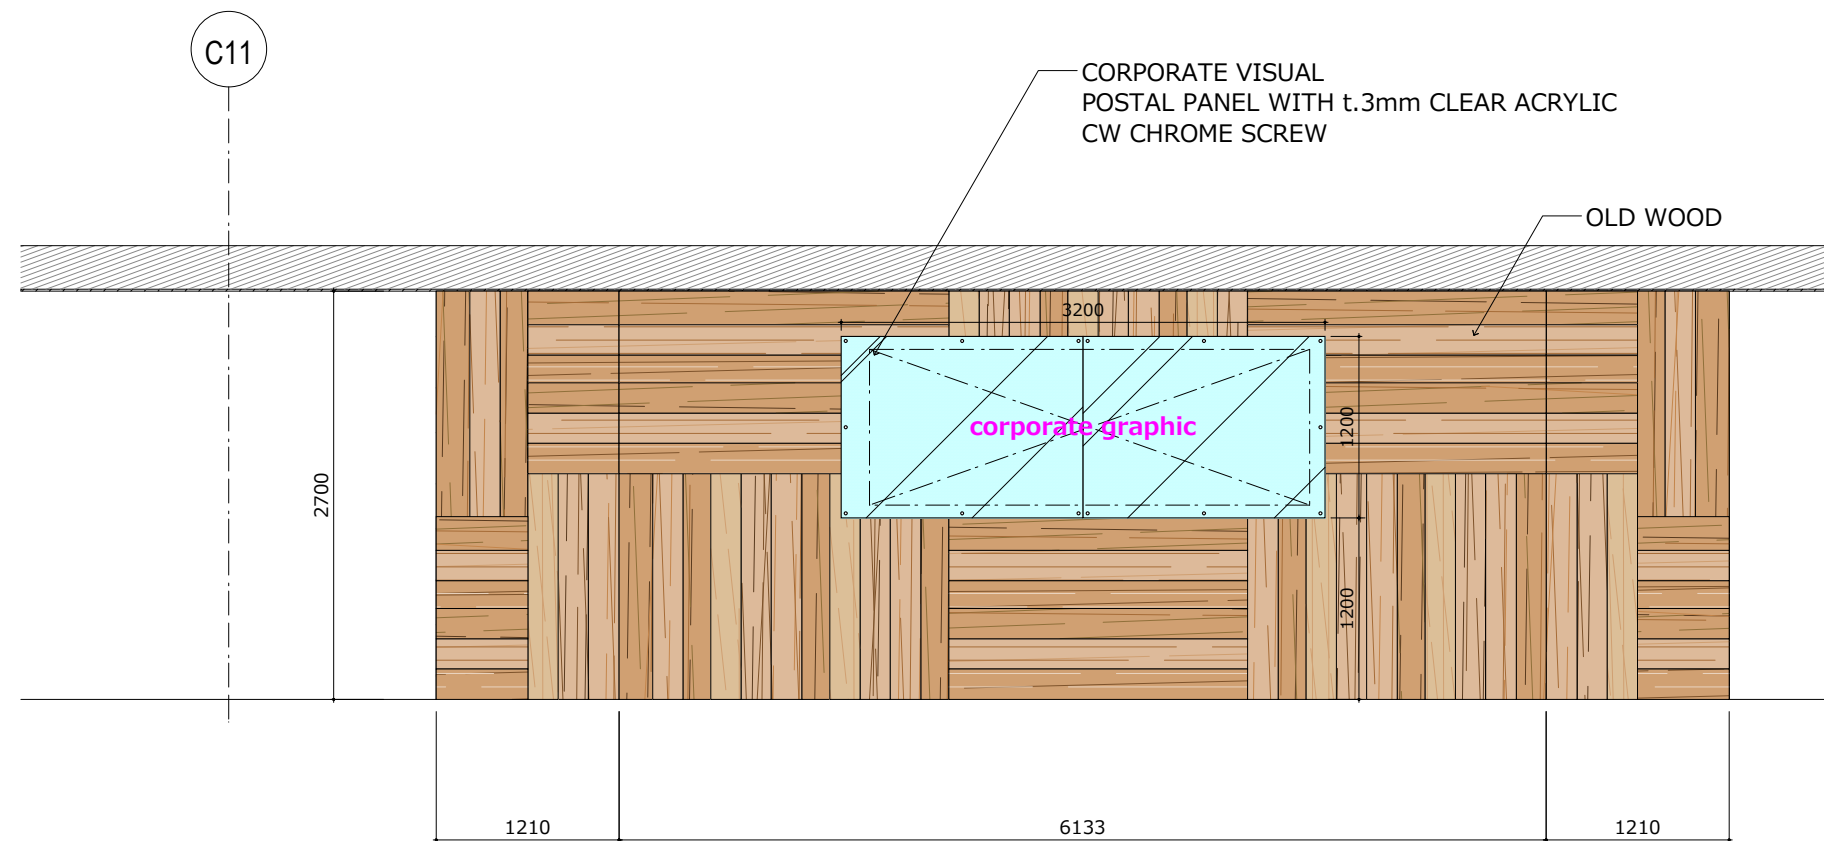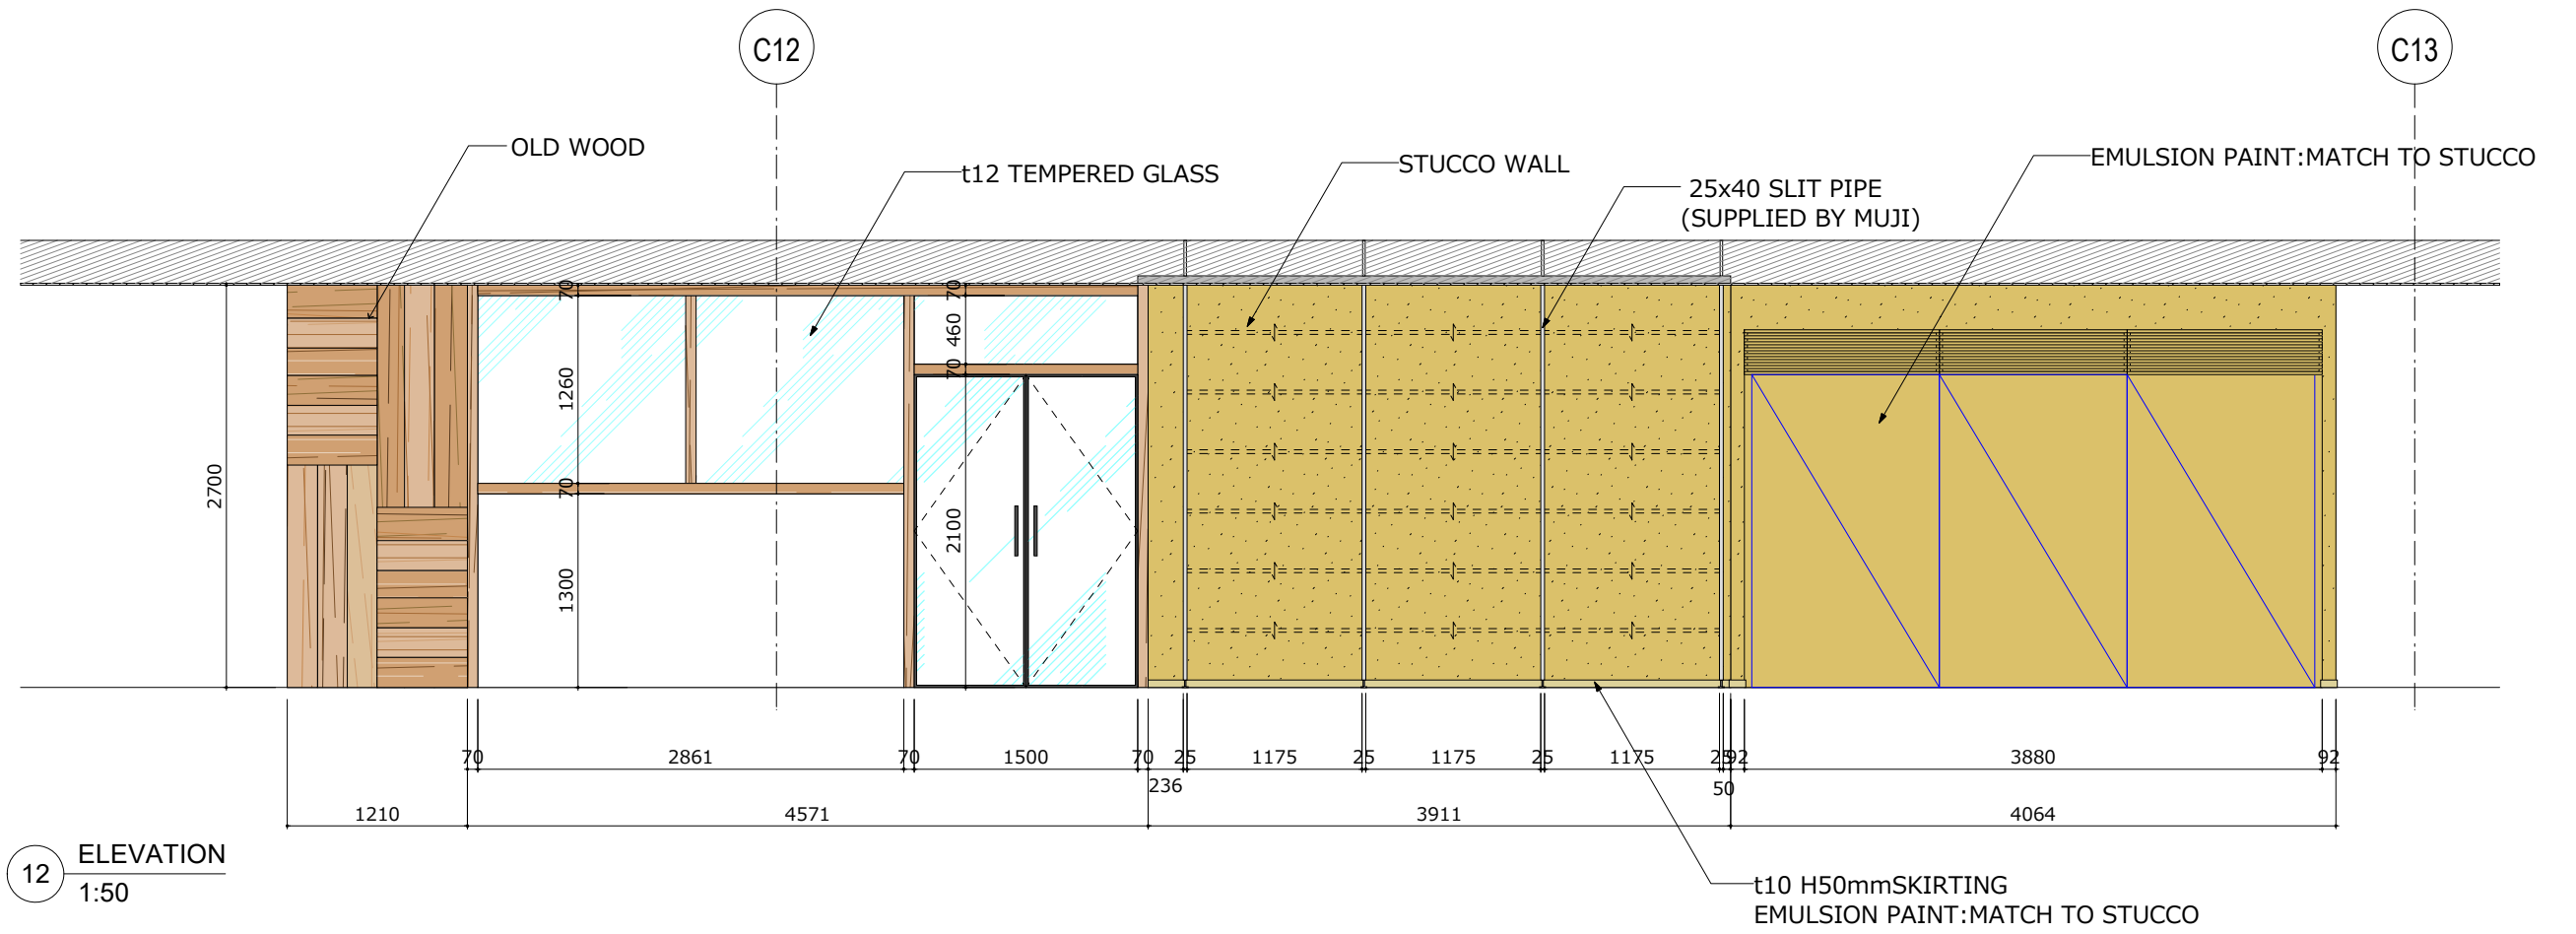


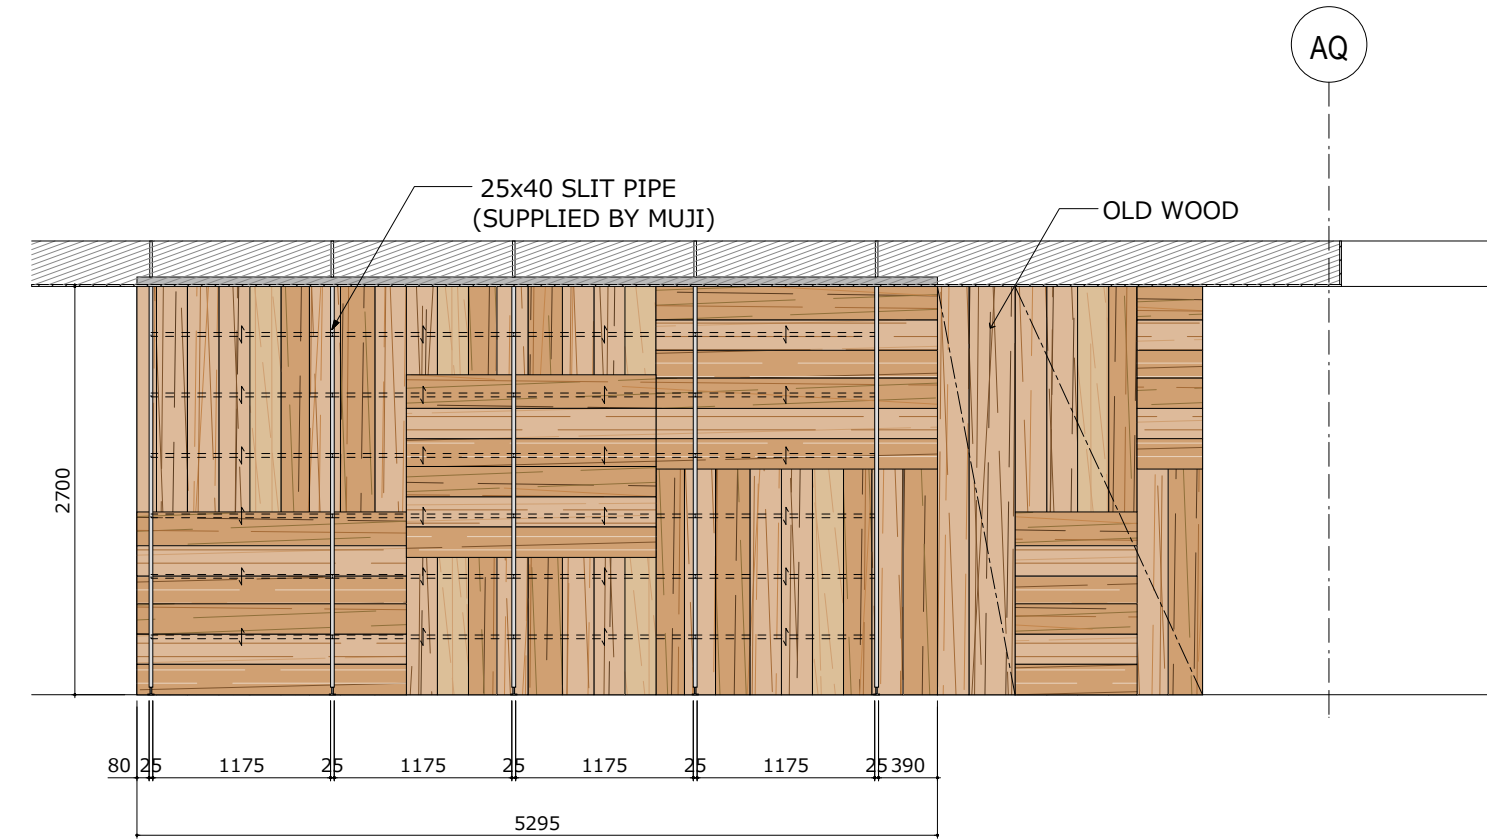





13 ELEVATION
1:50


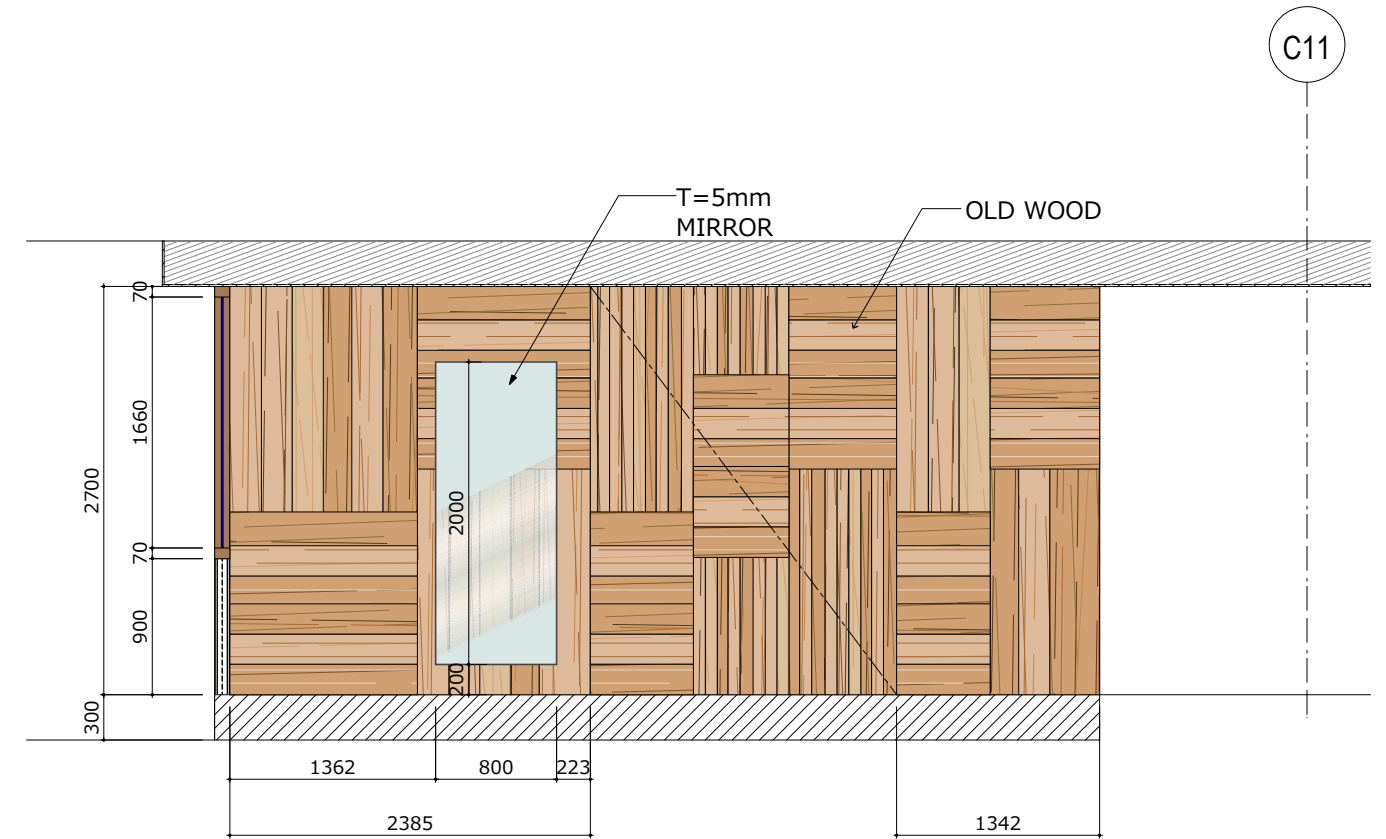



14 ELEVATION
1:50

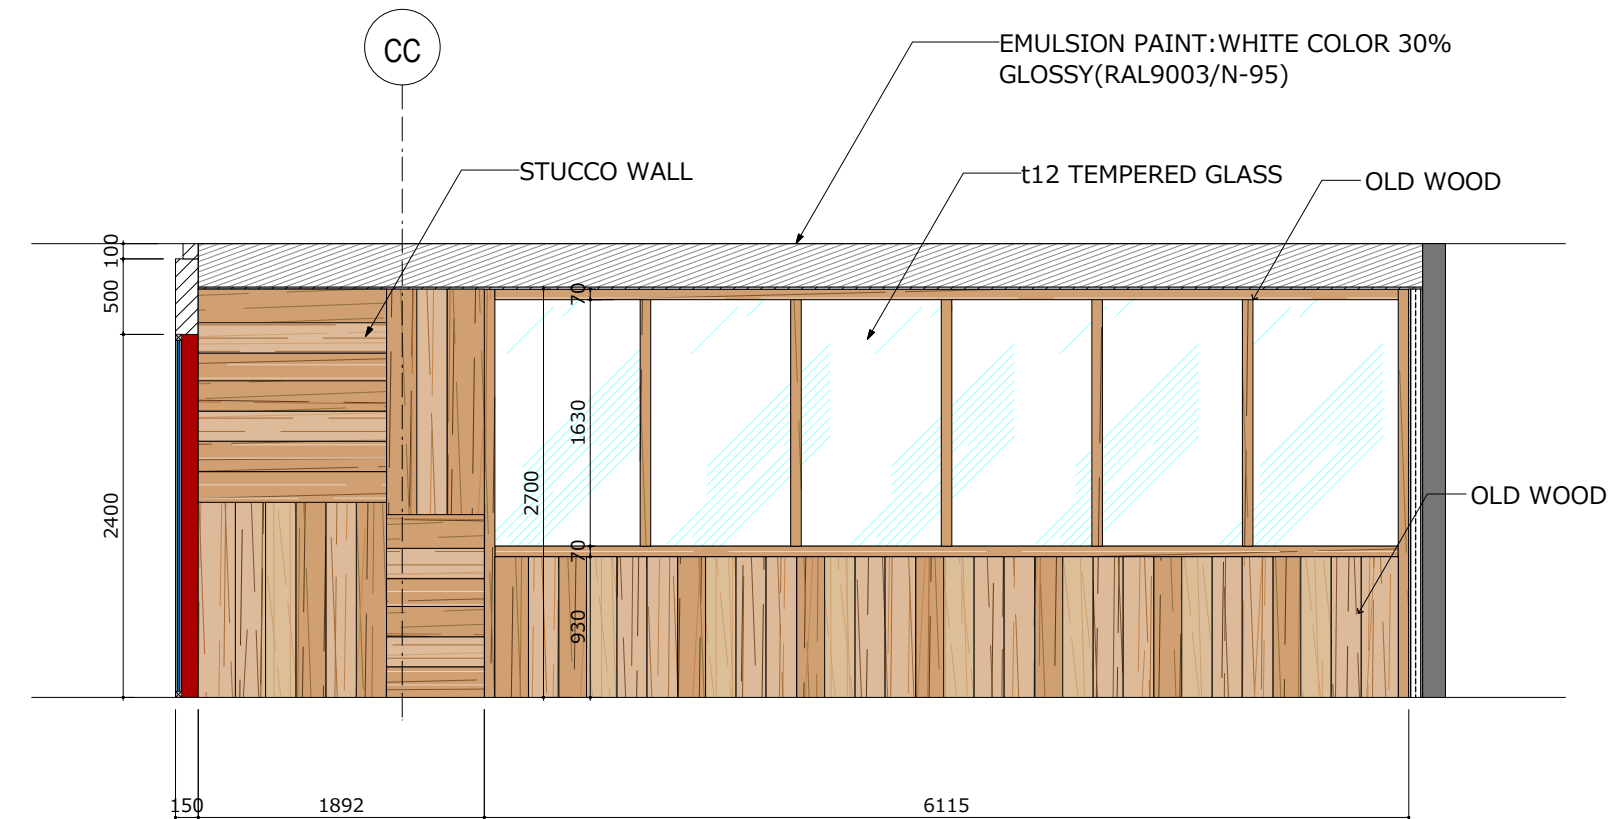




15 ELEVATION
1:50

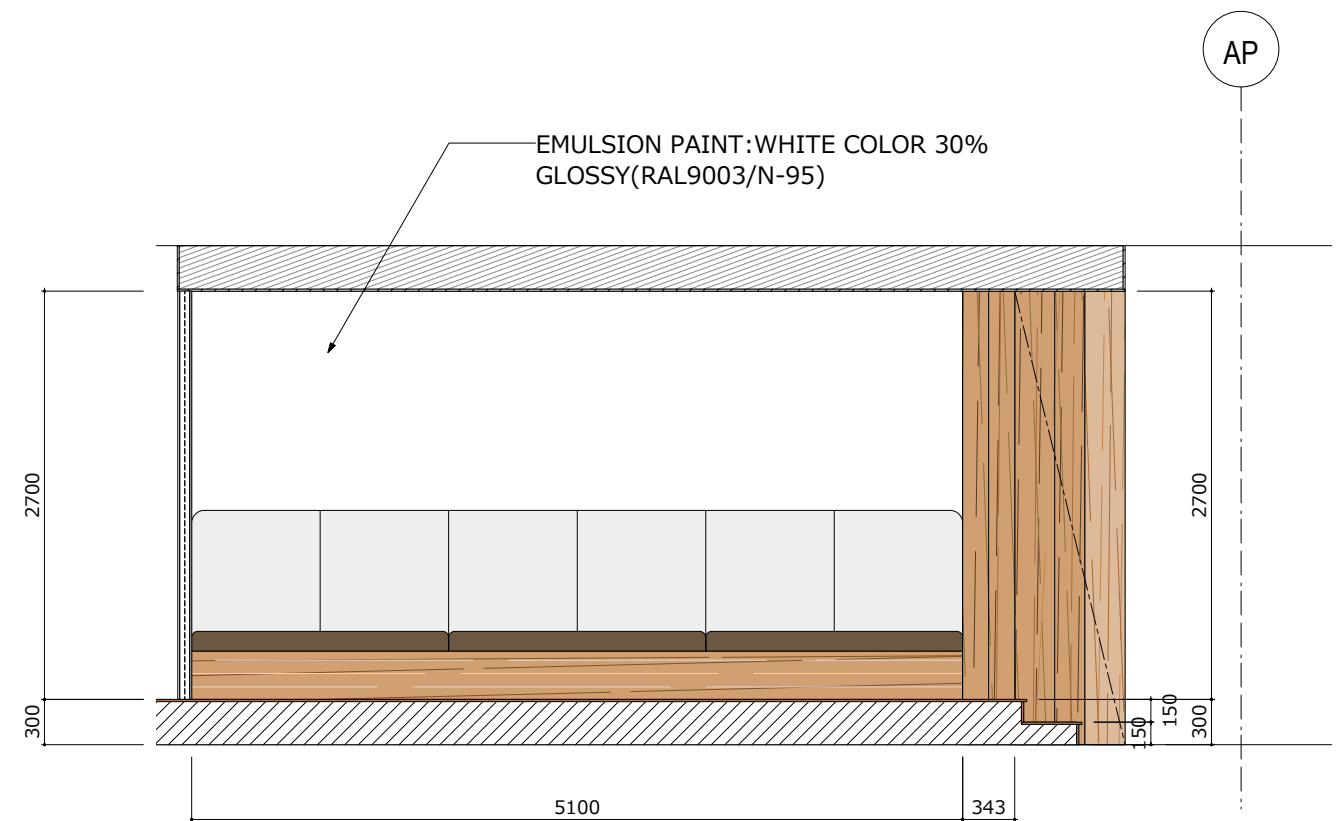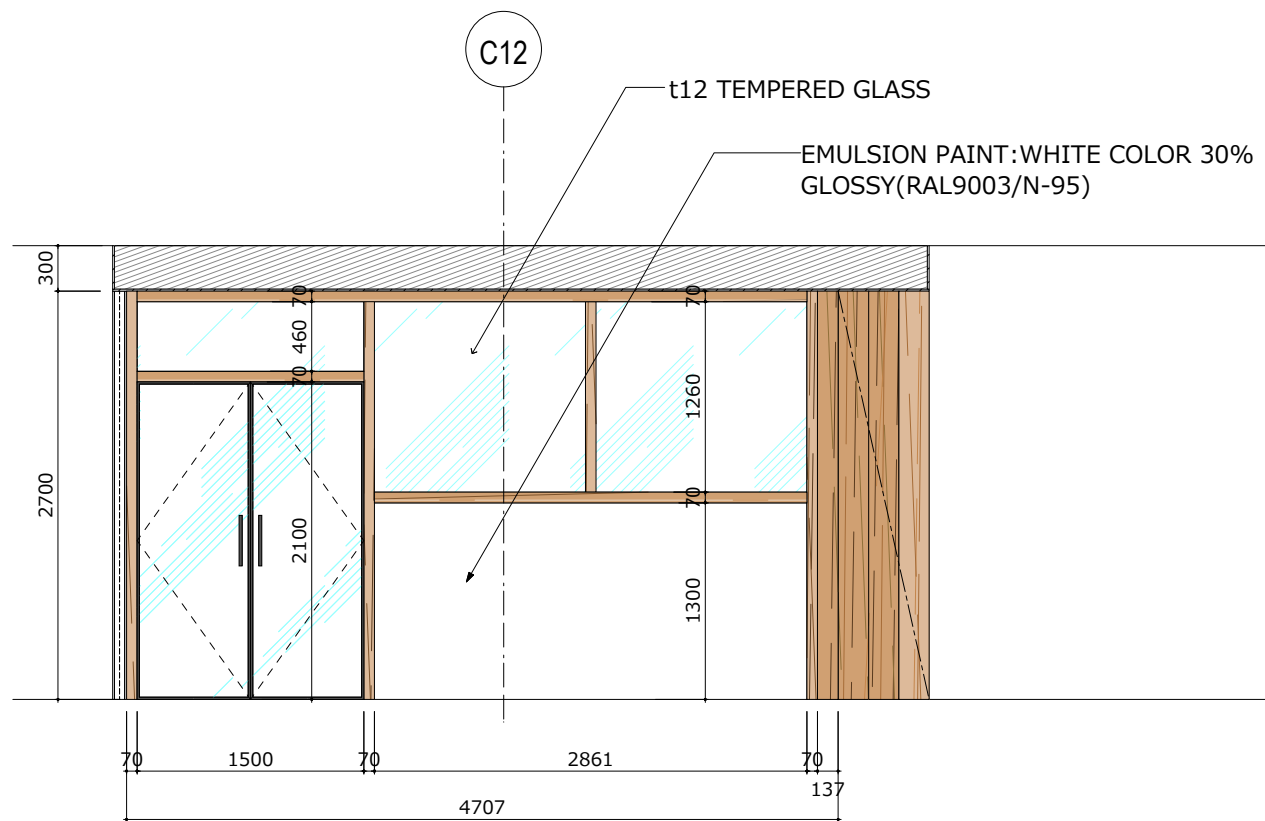
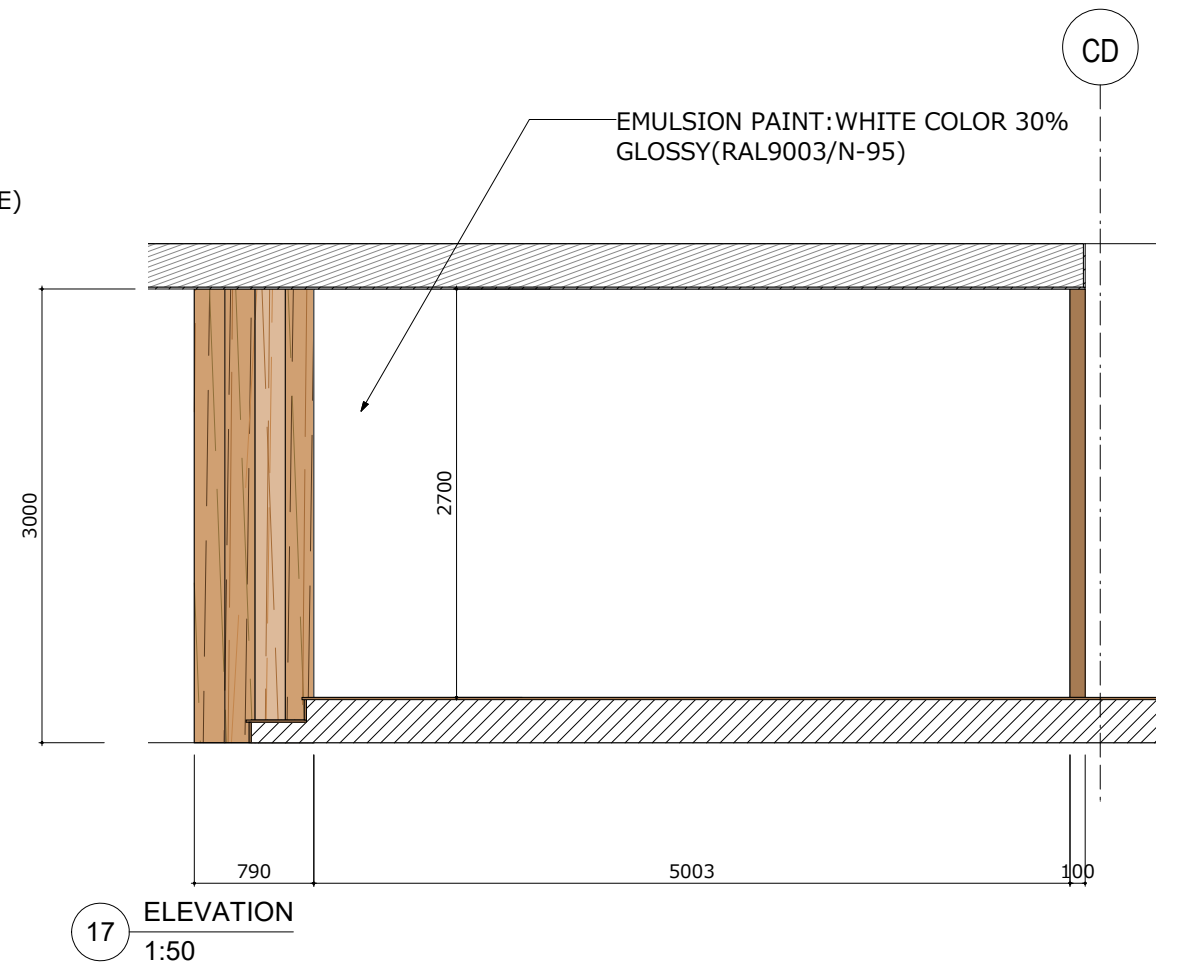
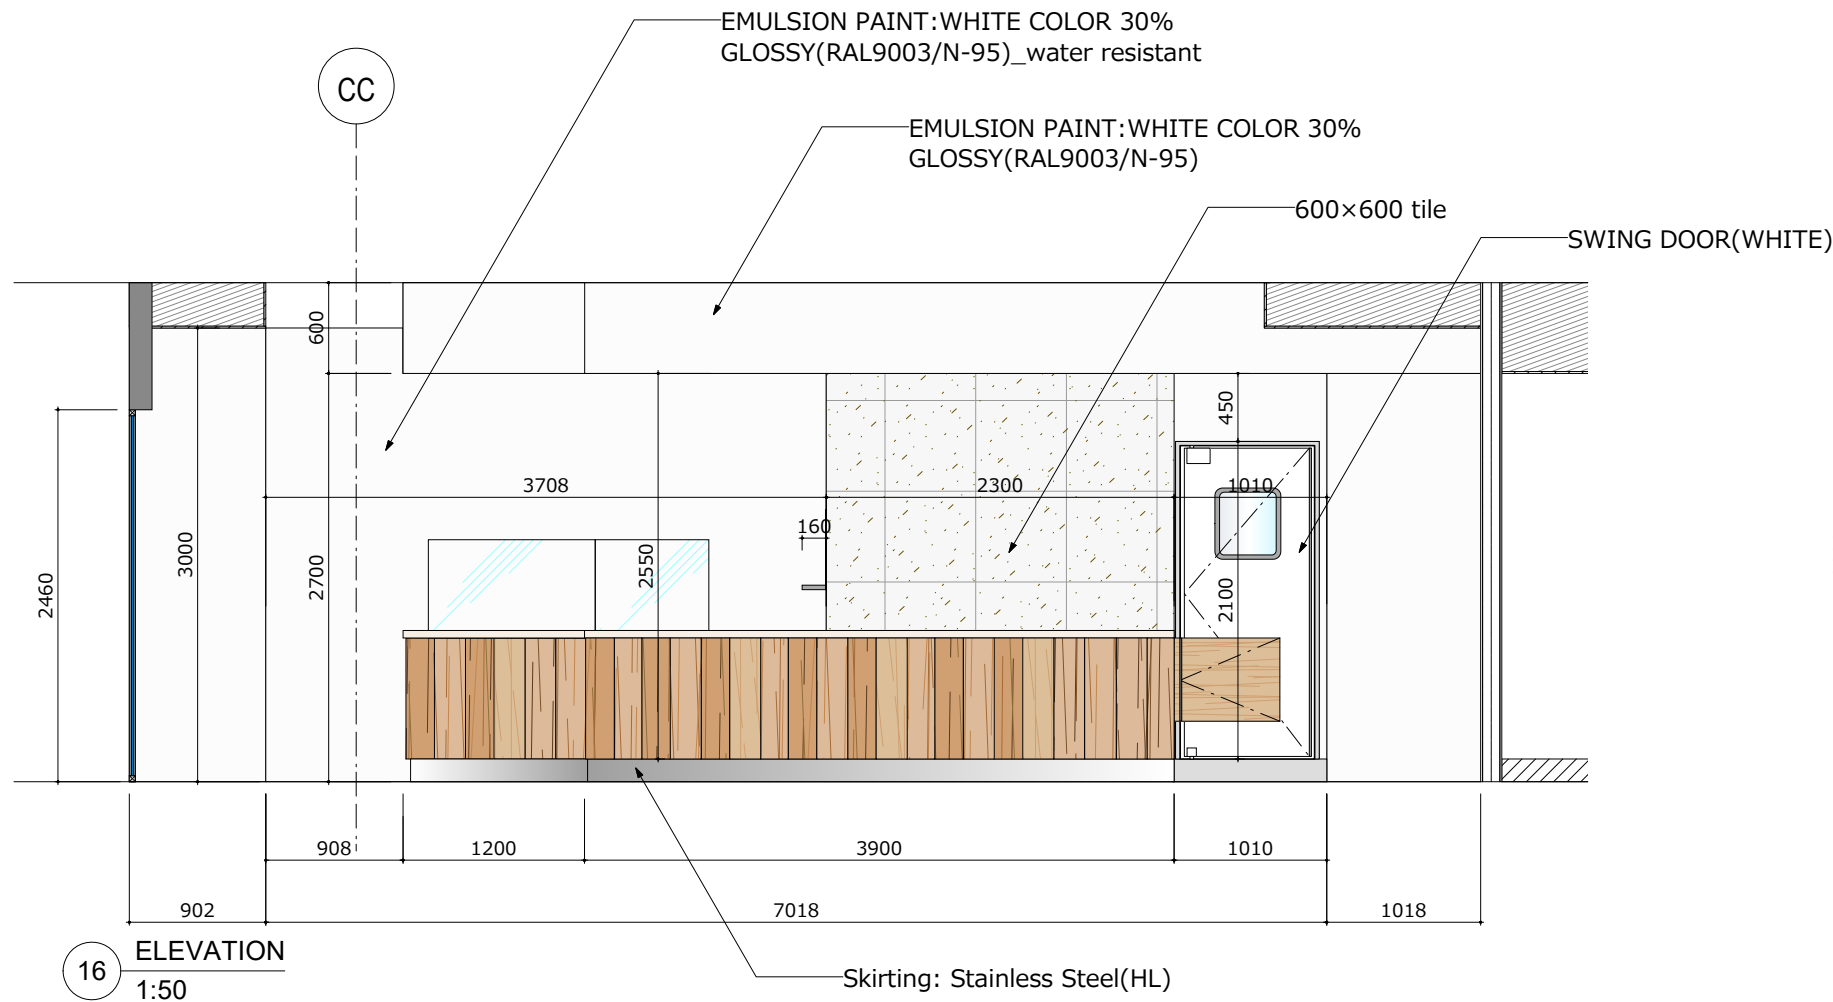


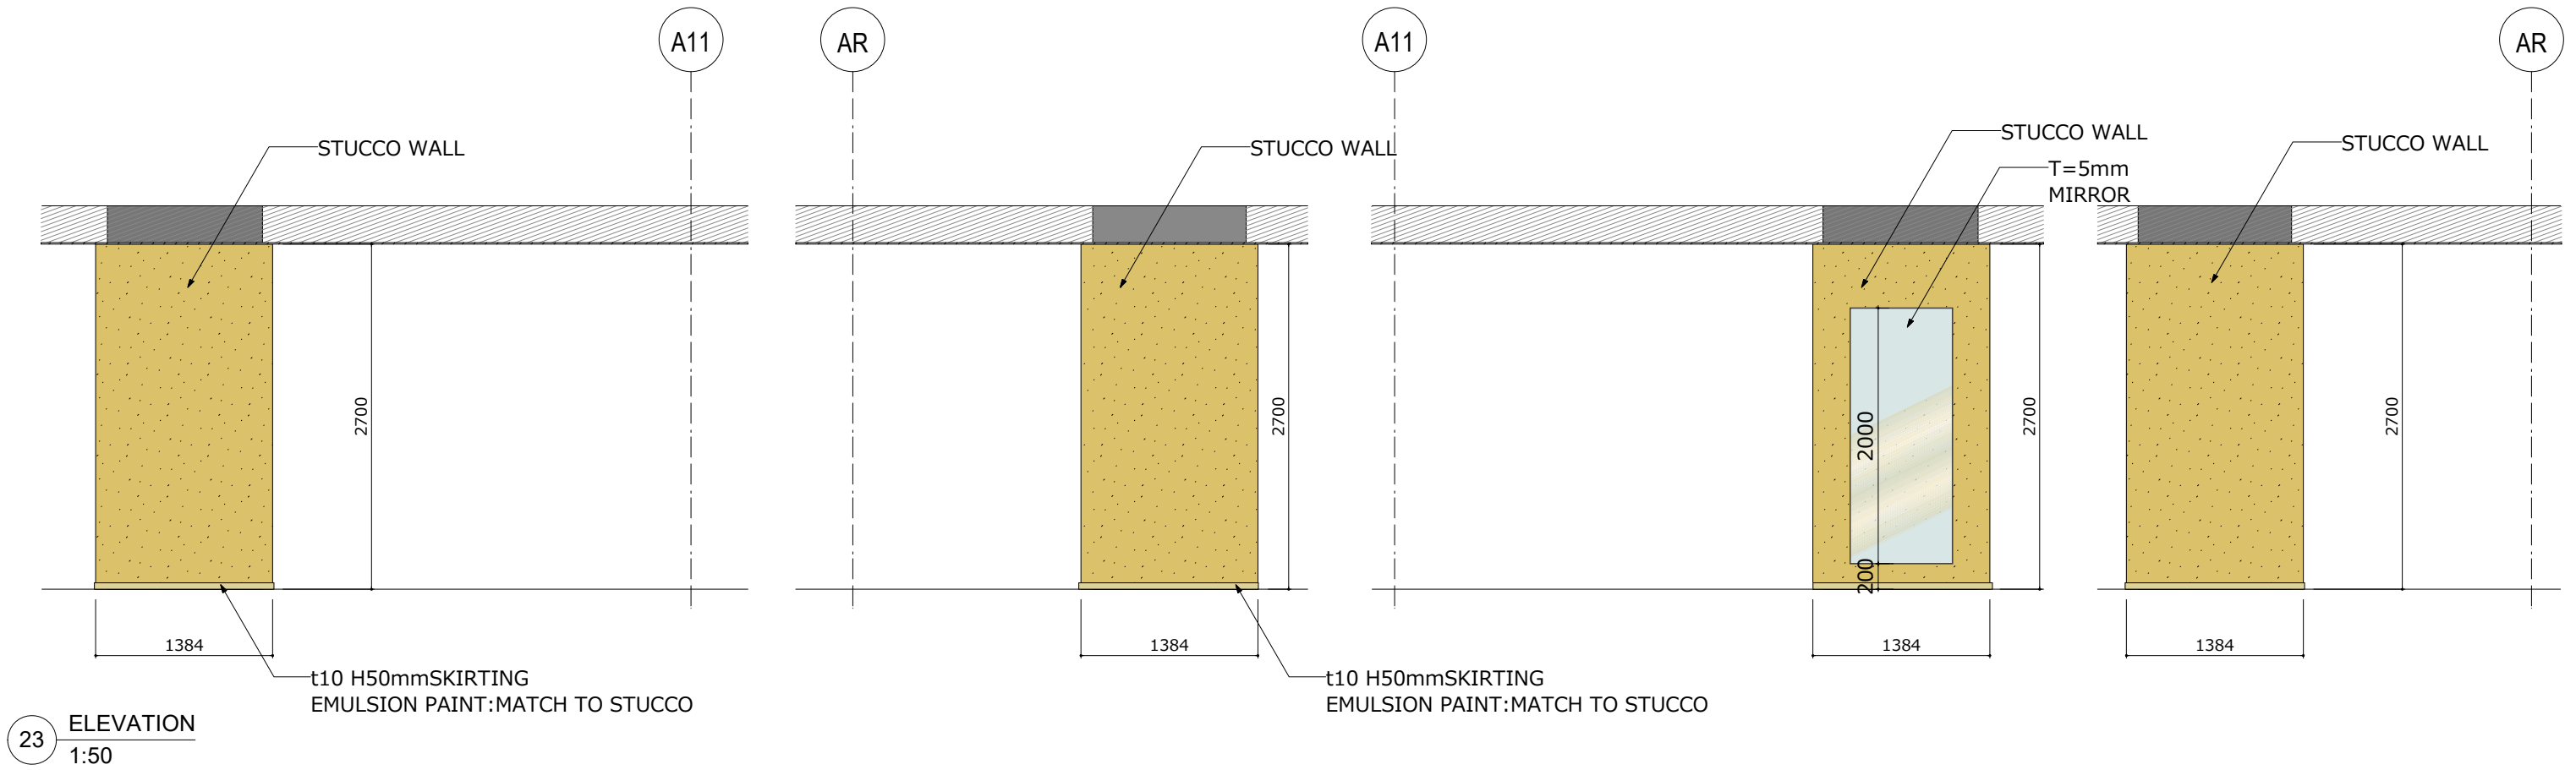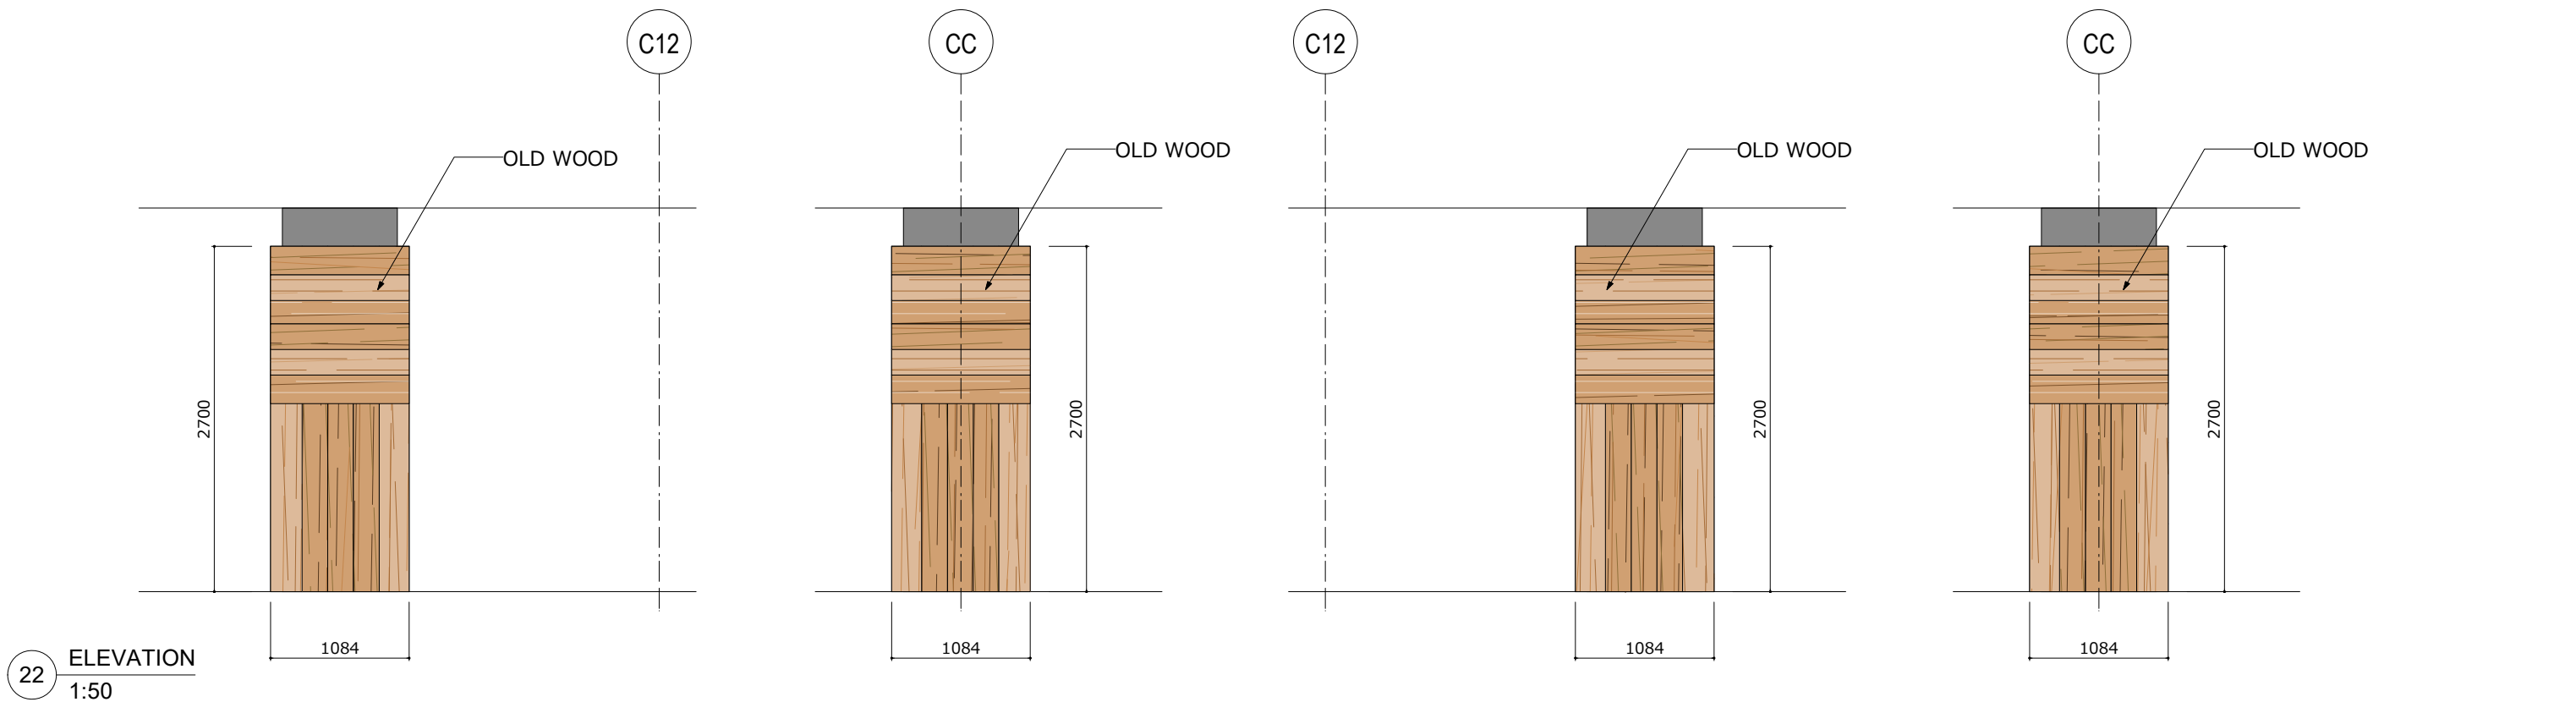



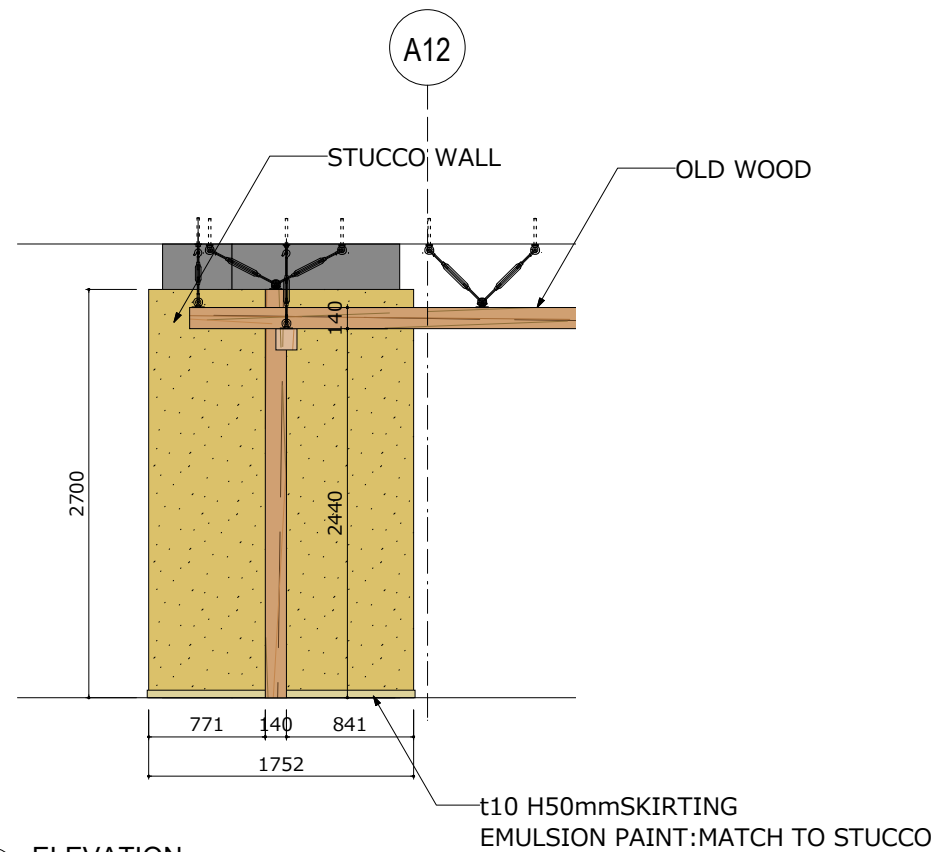


24 ELEVATION
1:50

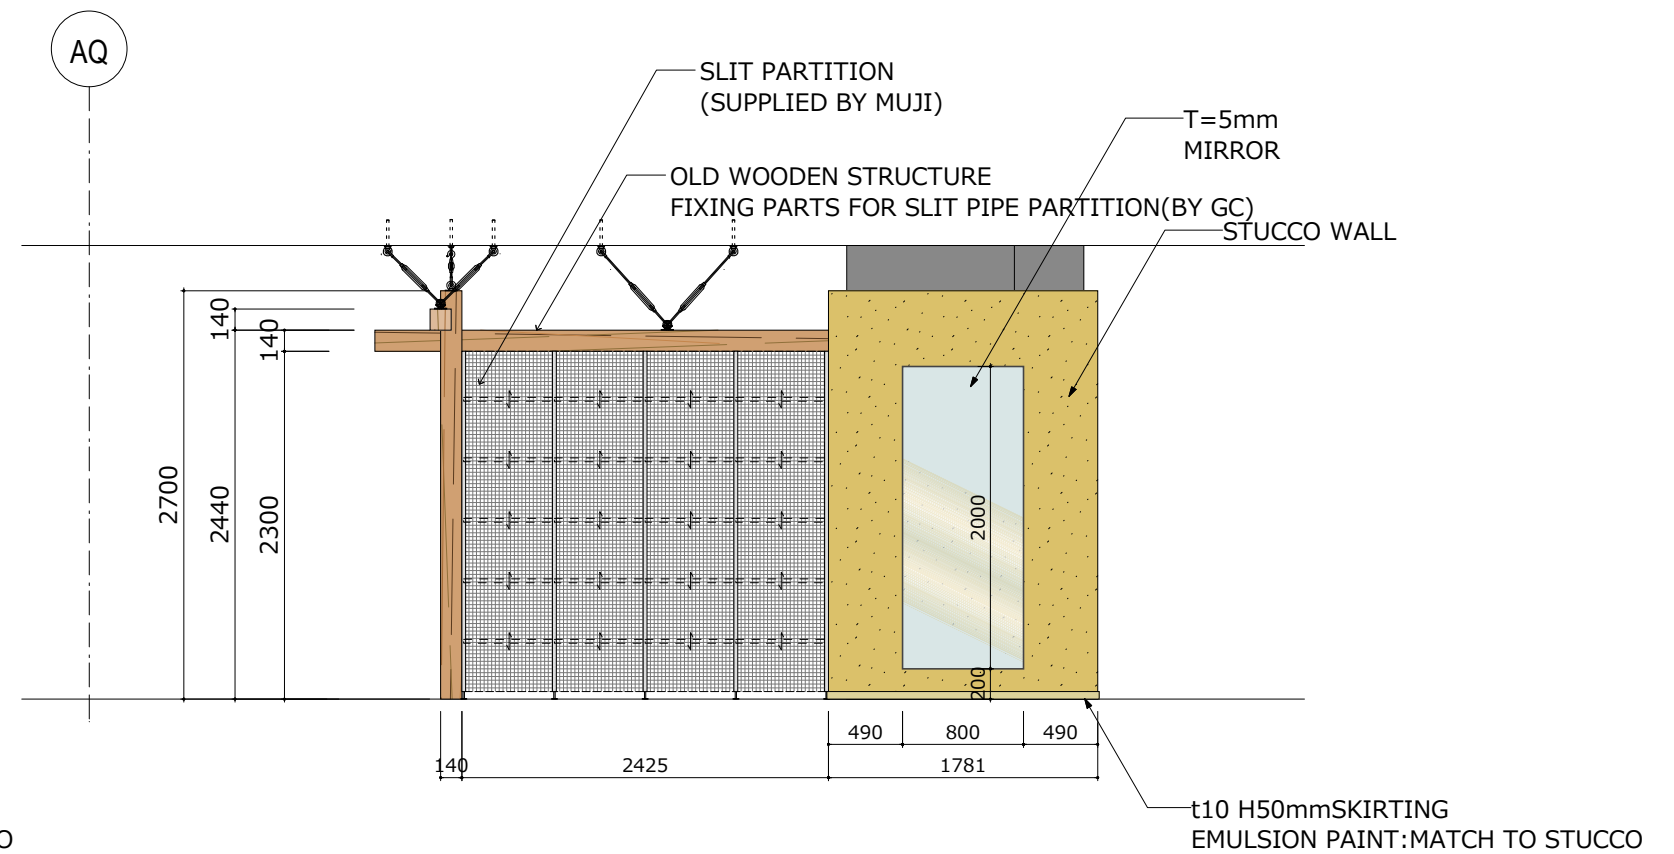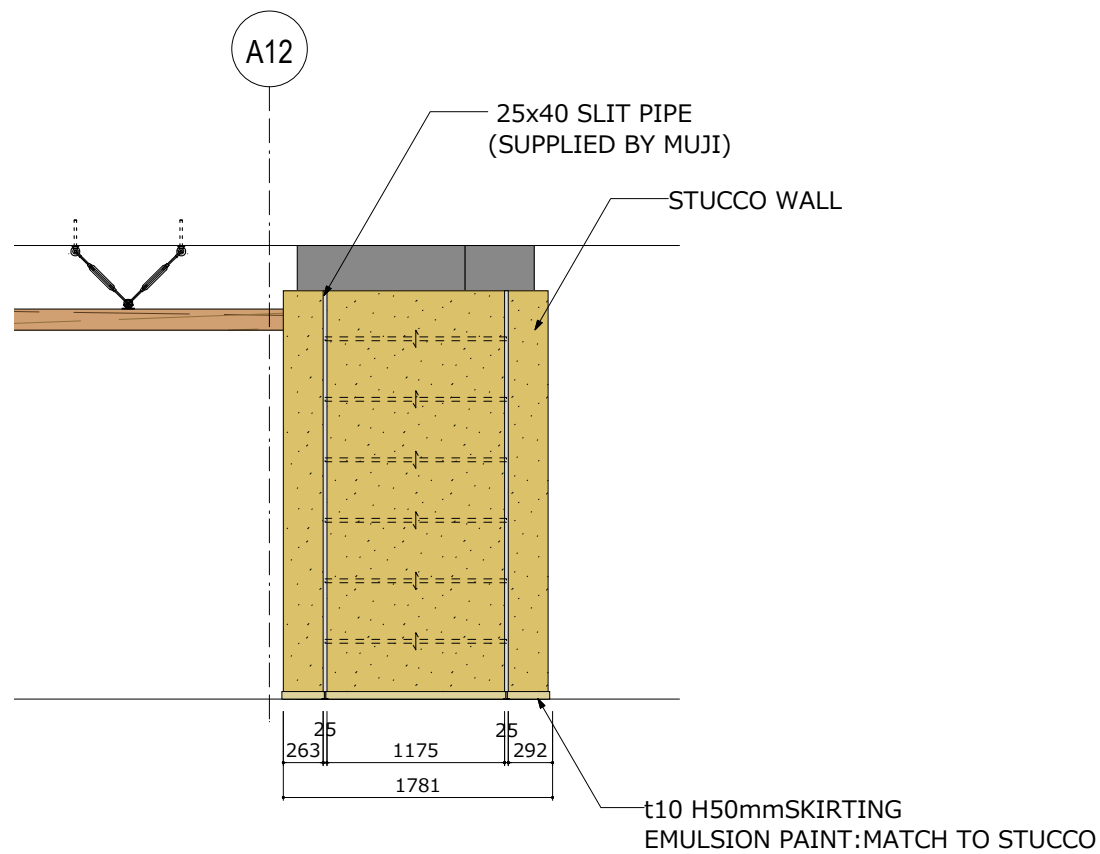
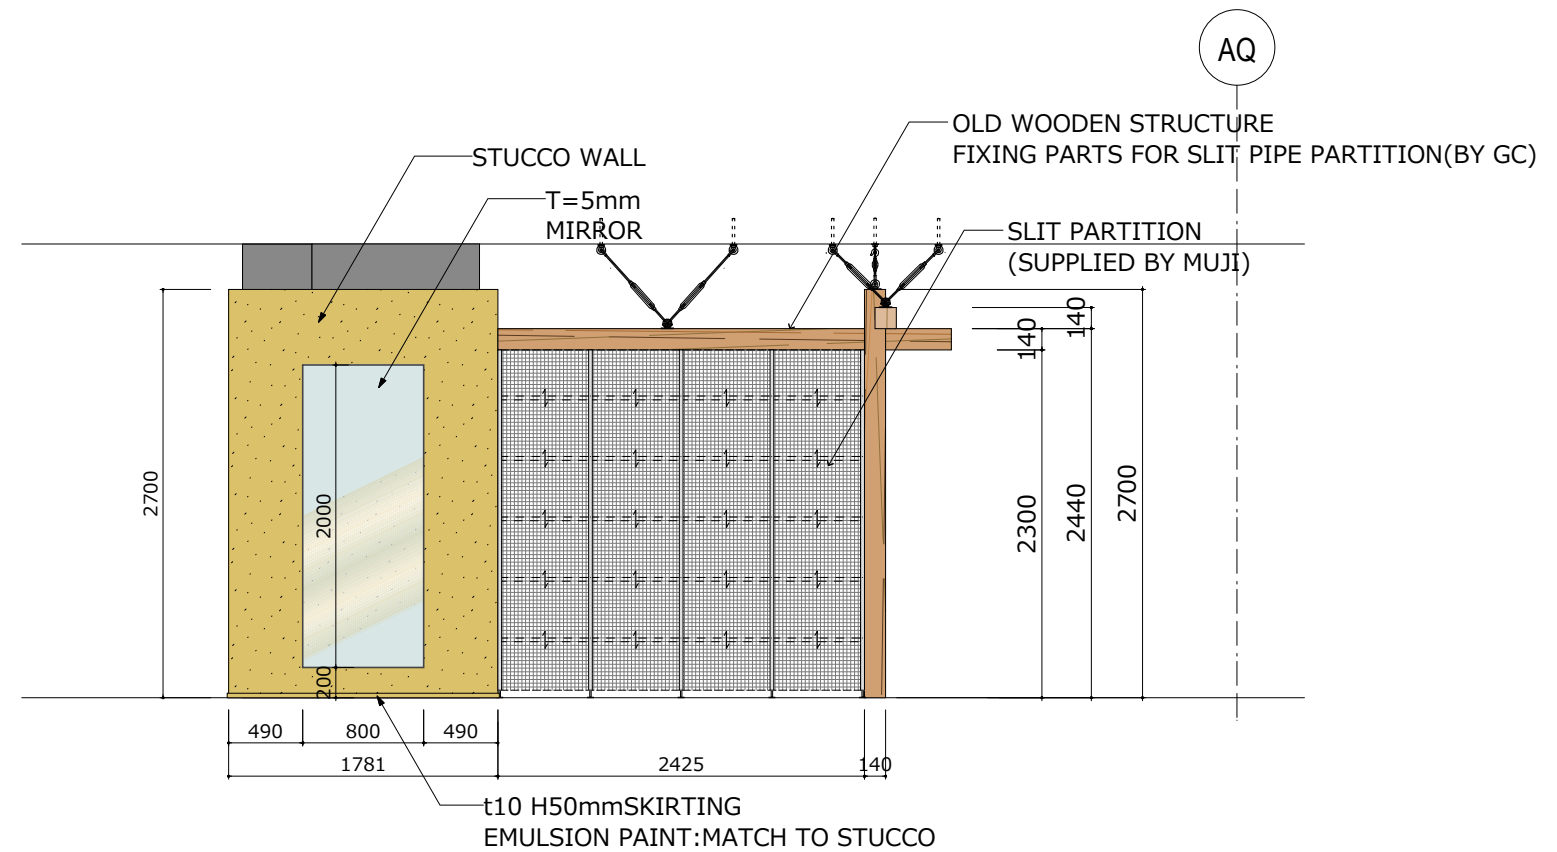


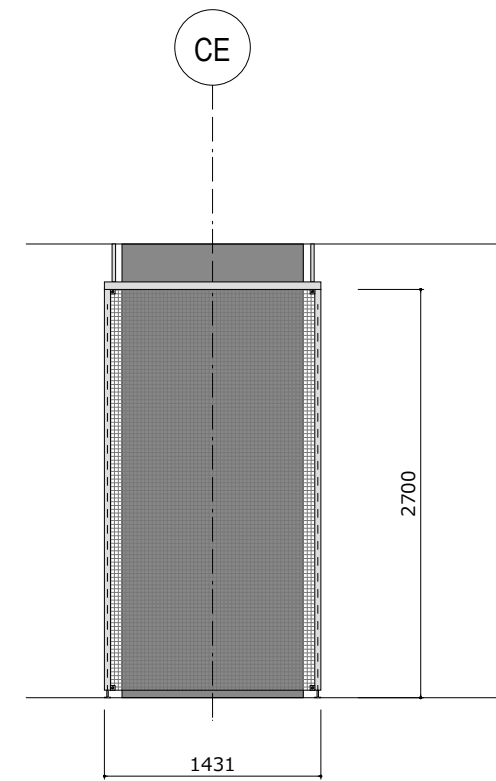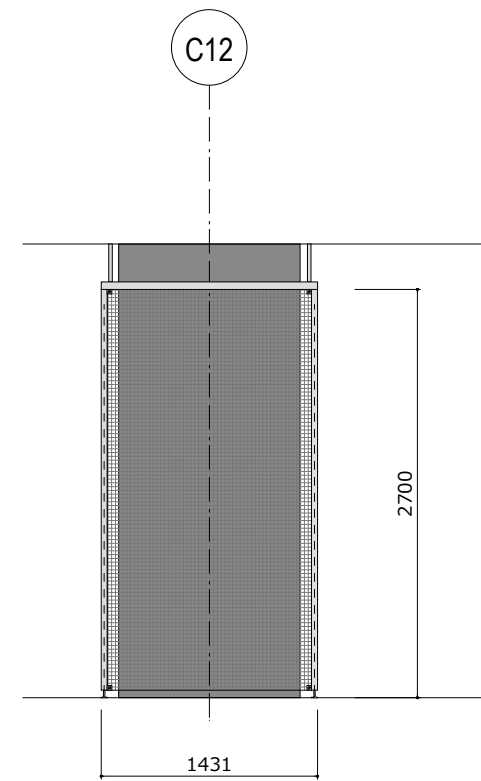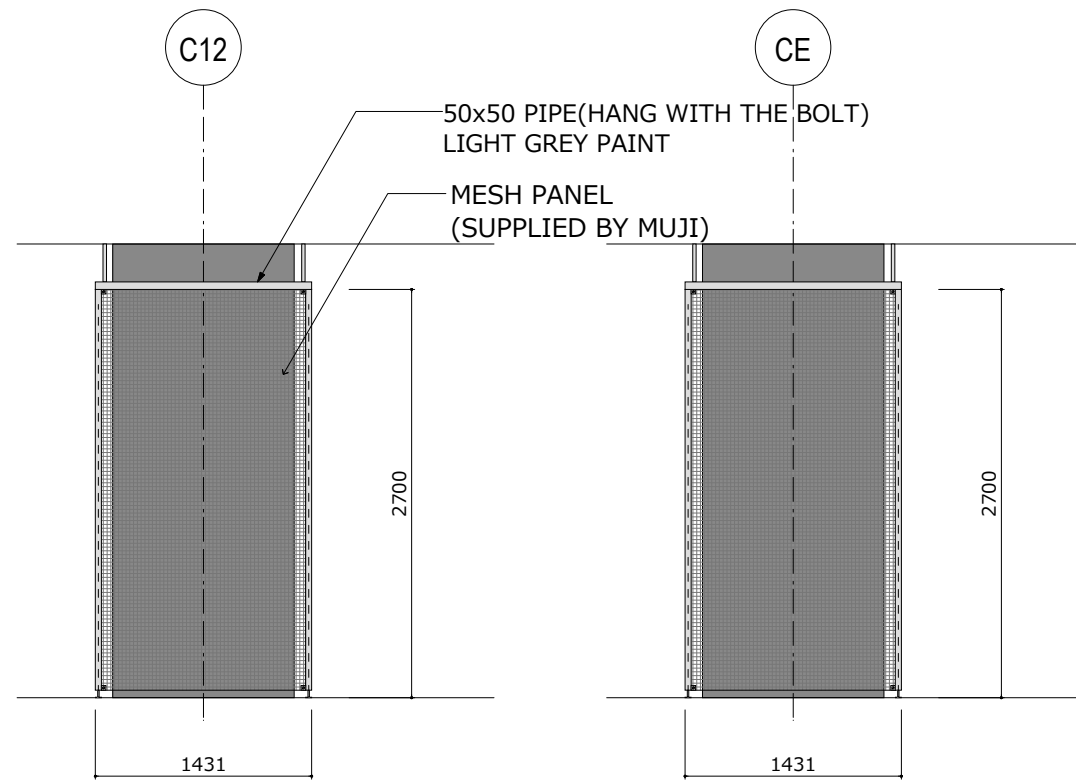



25 ELEVATION
1:50

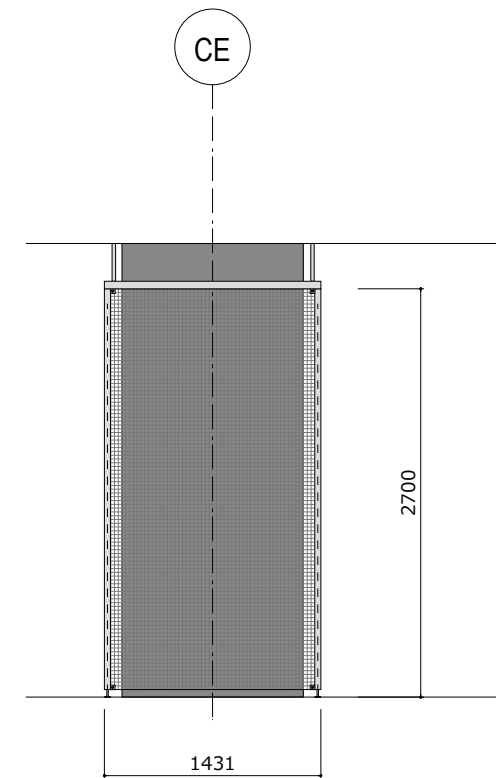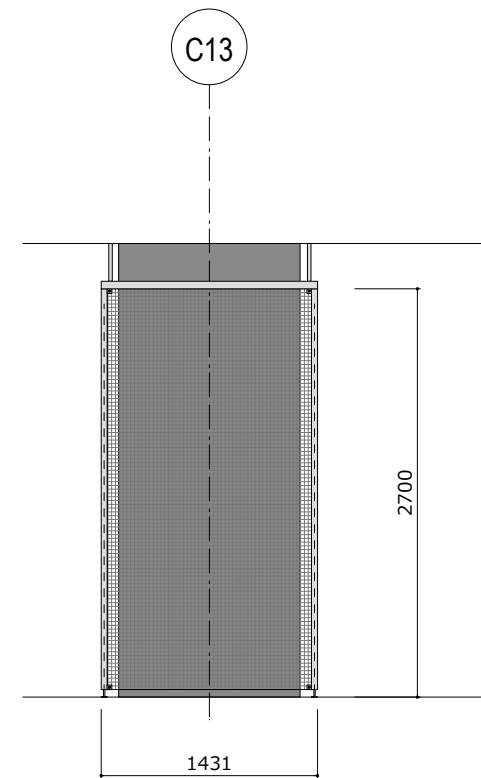
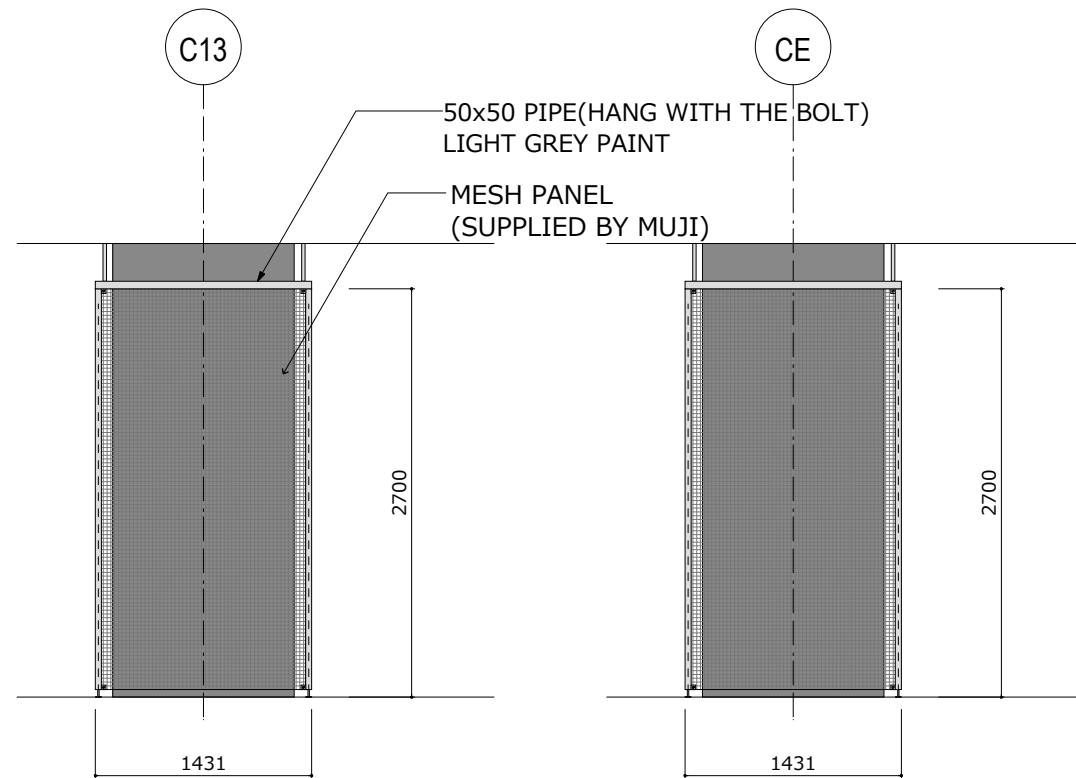


26 ELEVATION
1:50

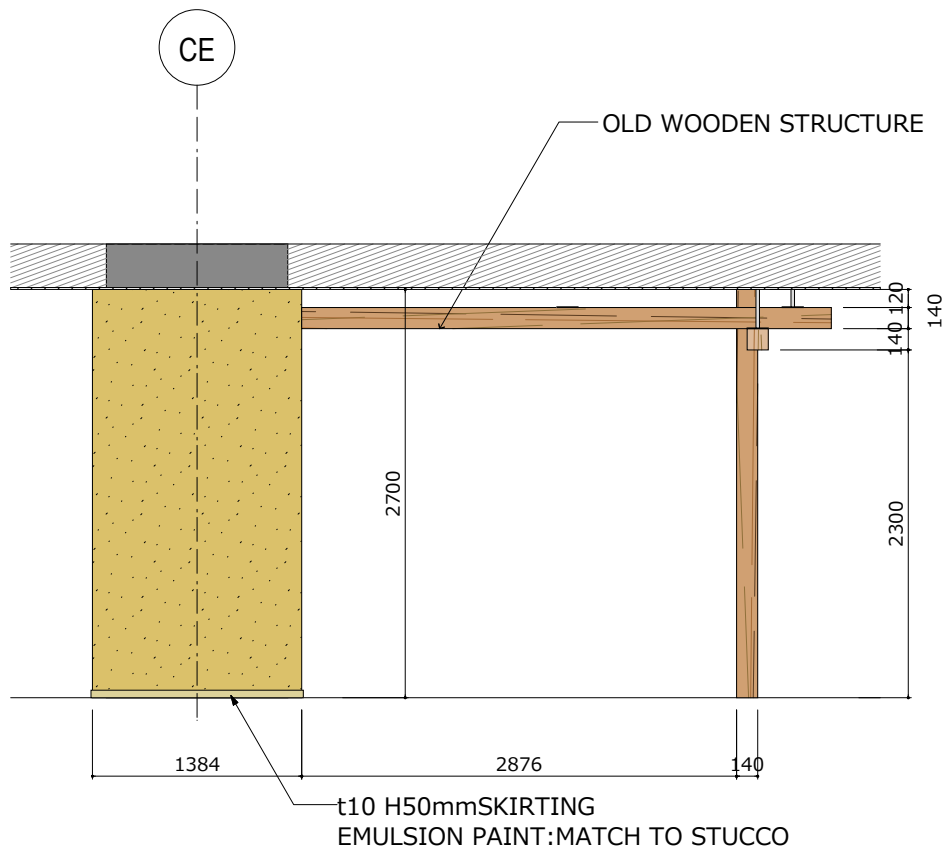
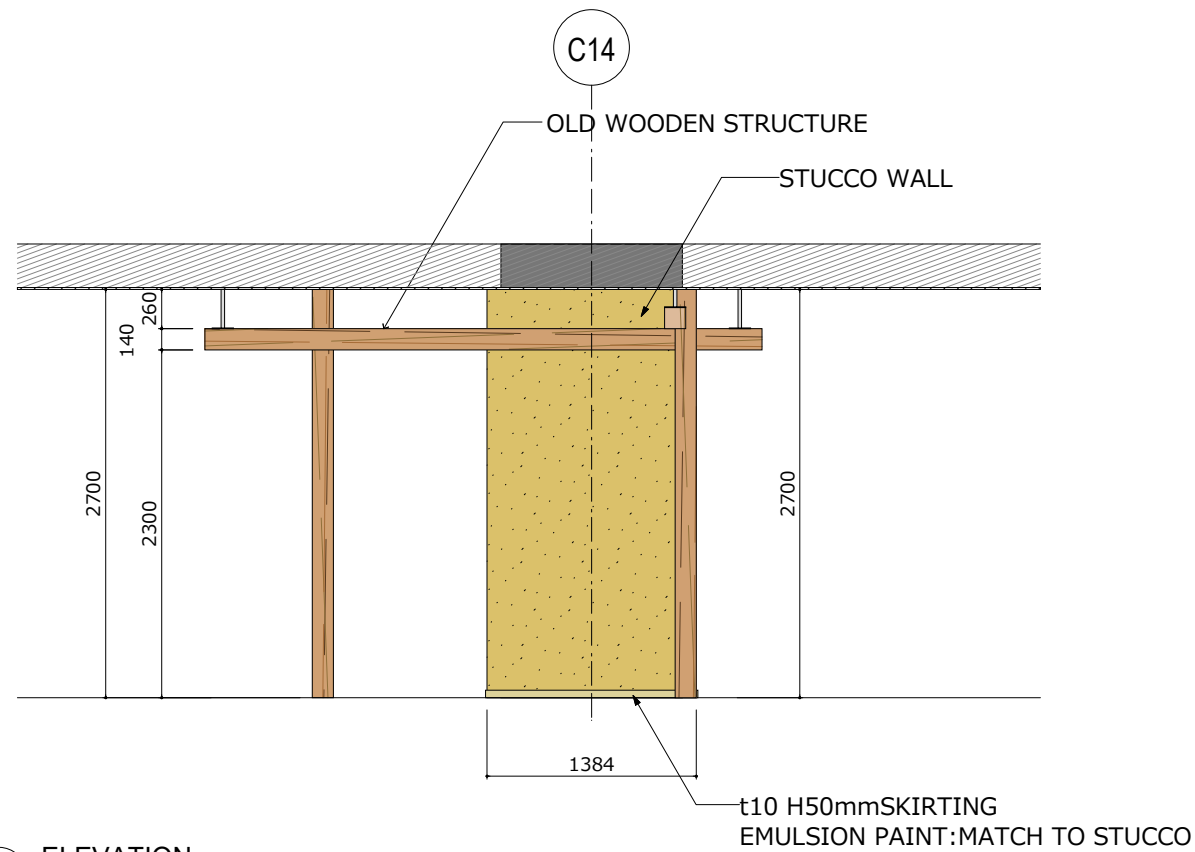


27 ELEVATION
1:50

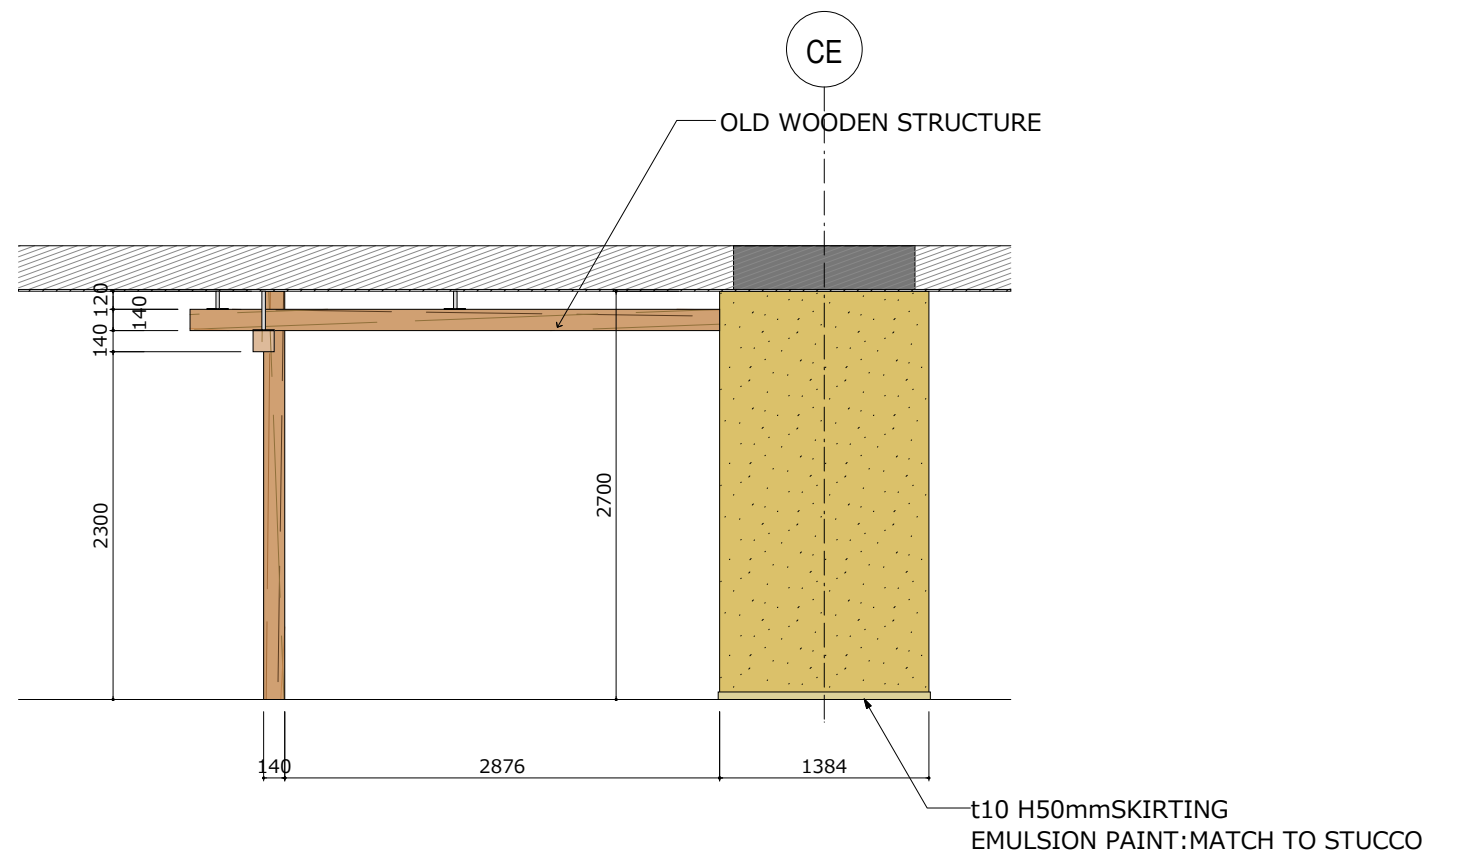
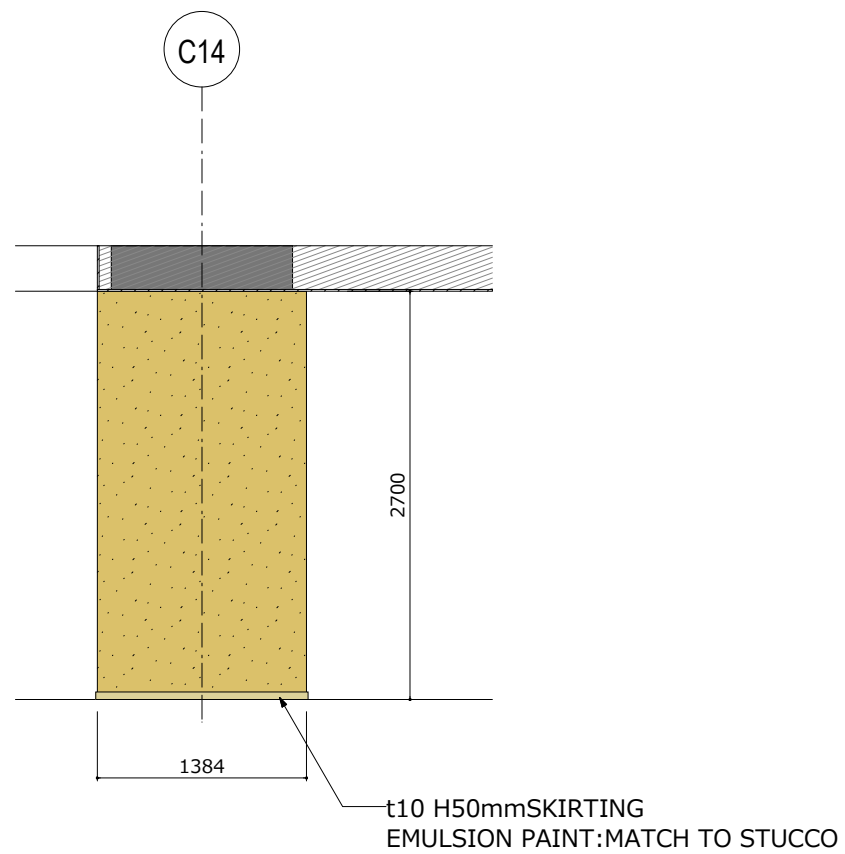


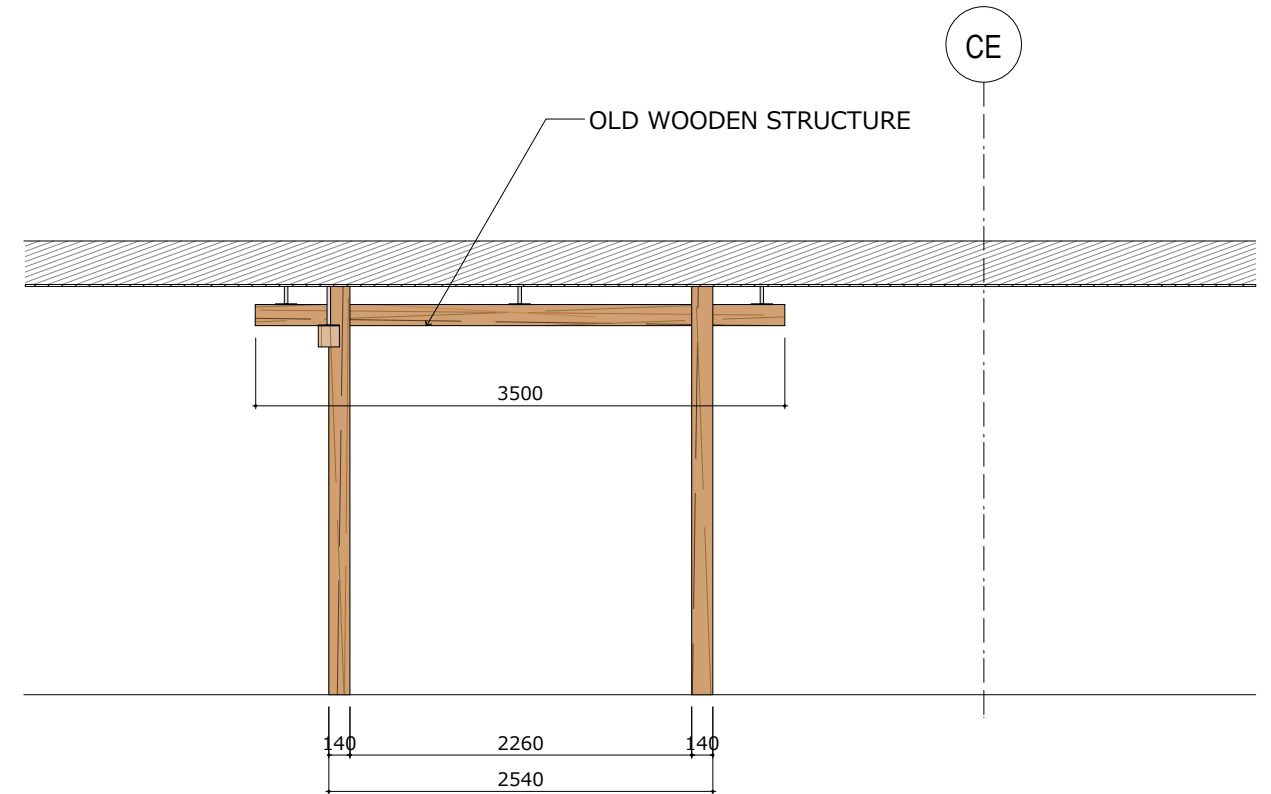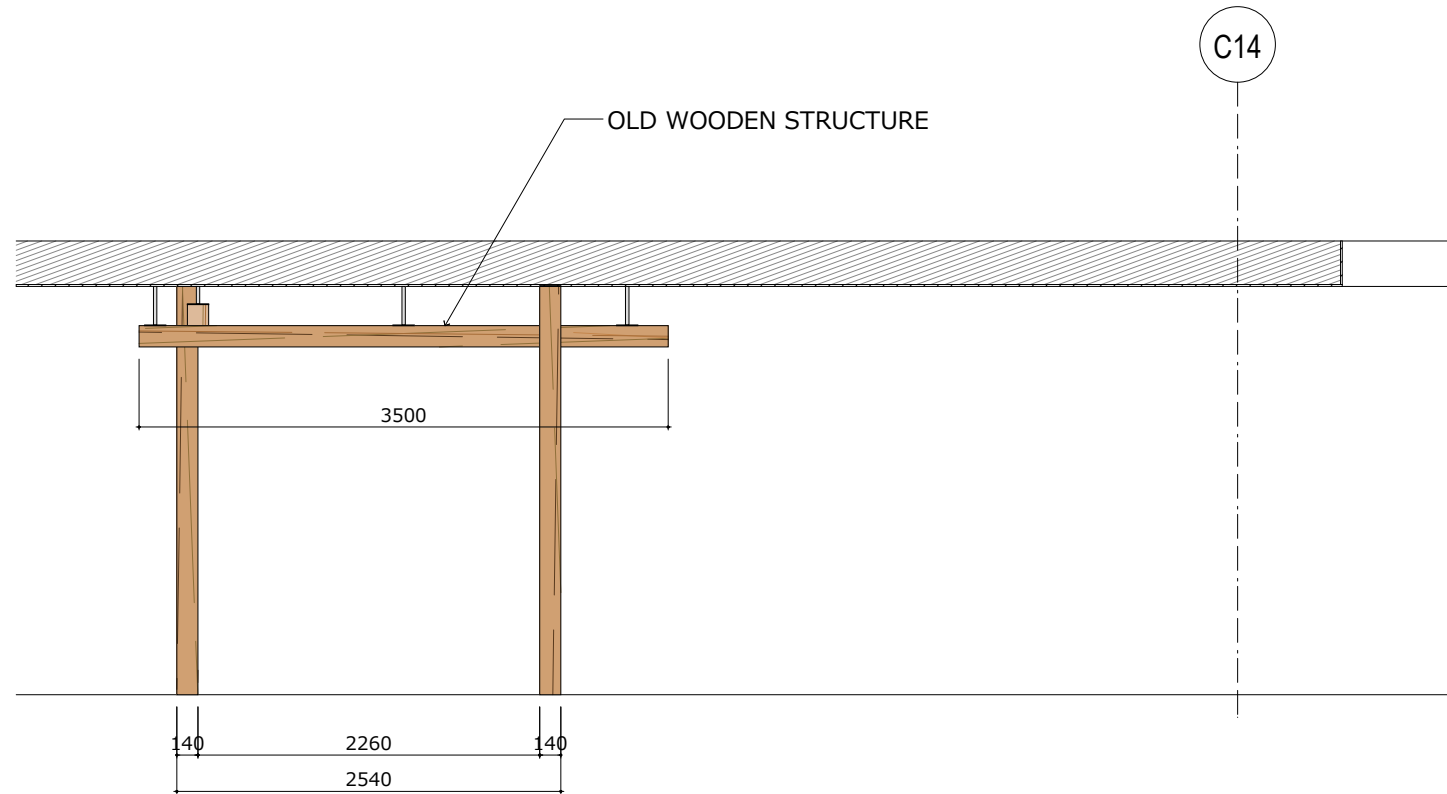


28 ELEVATION
1:50

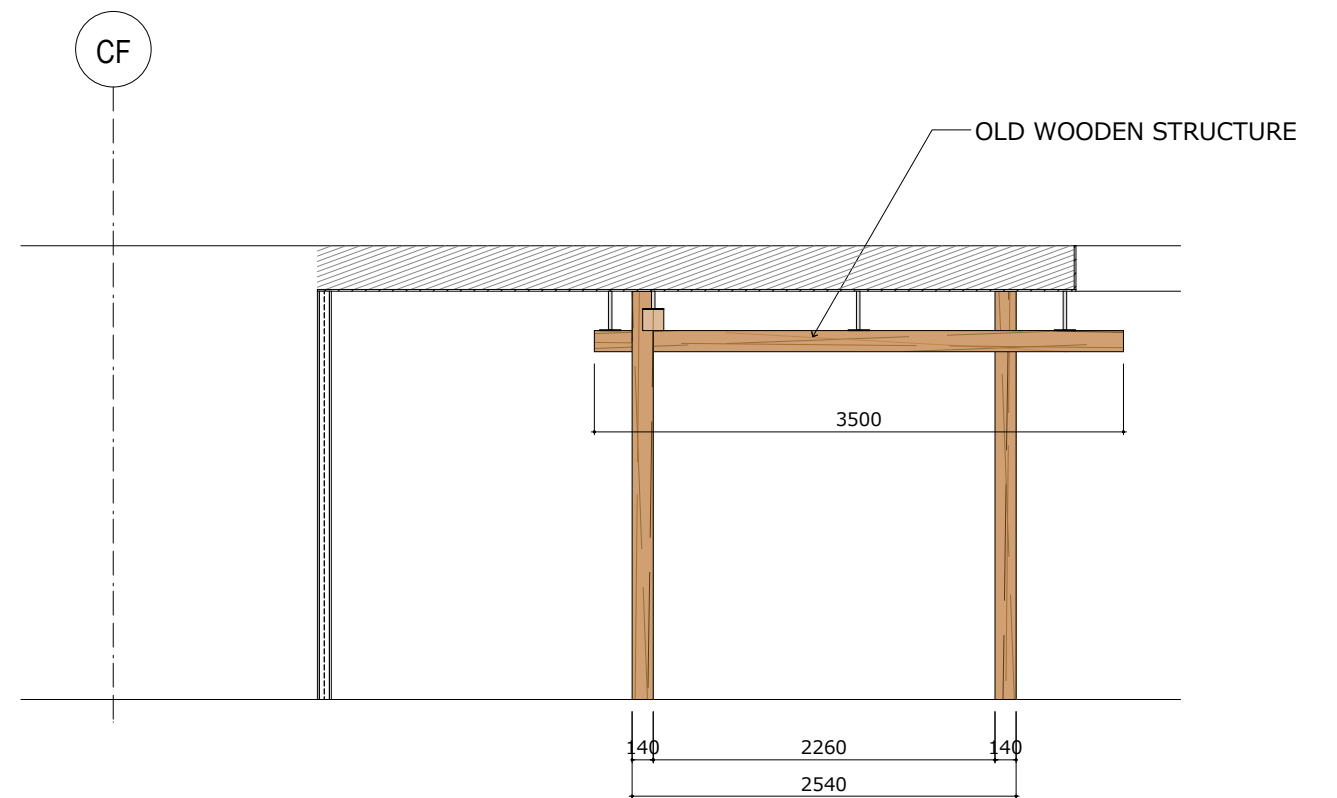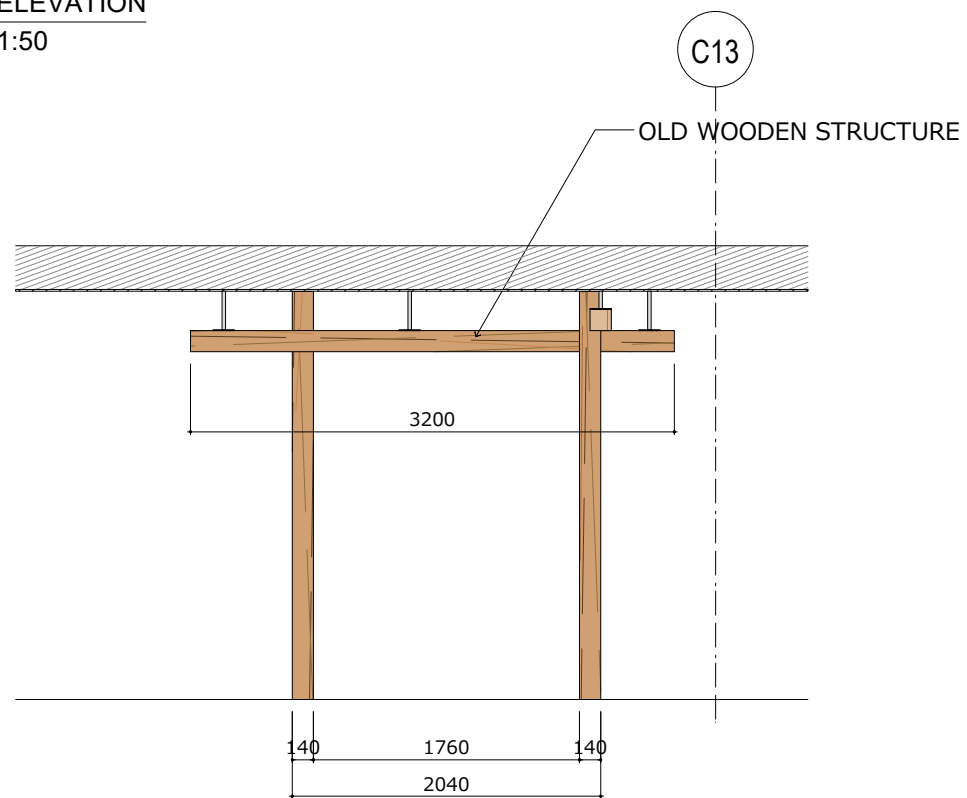


29 ELEVATION
1:50

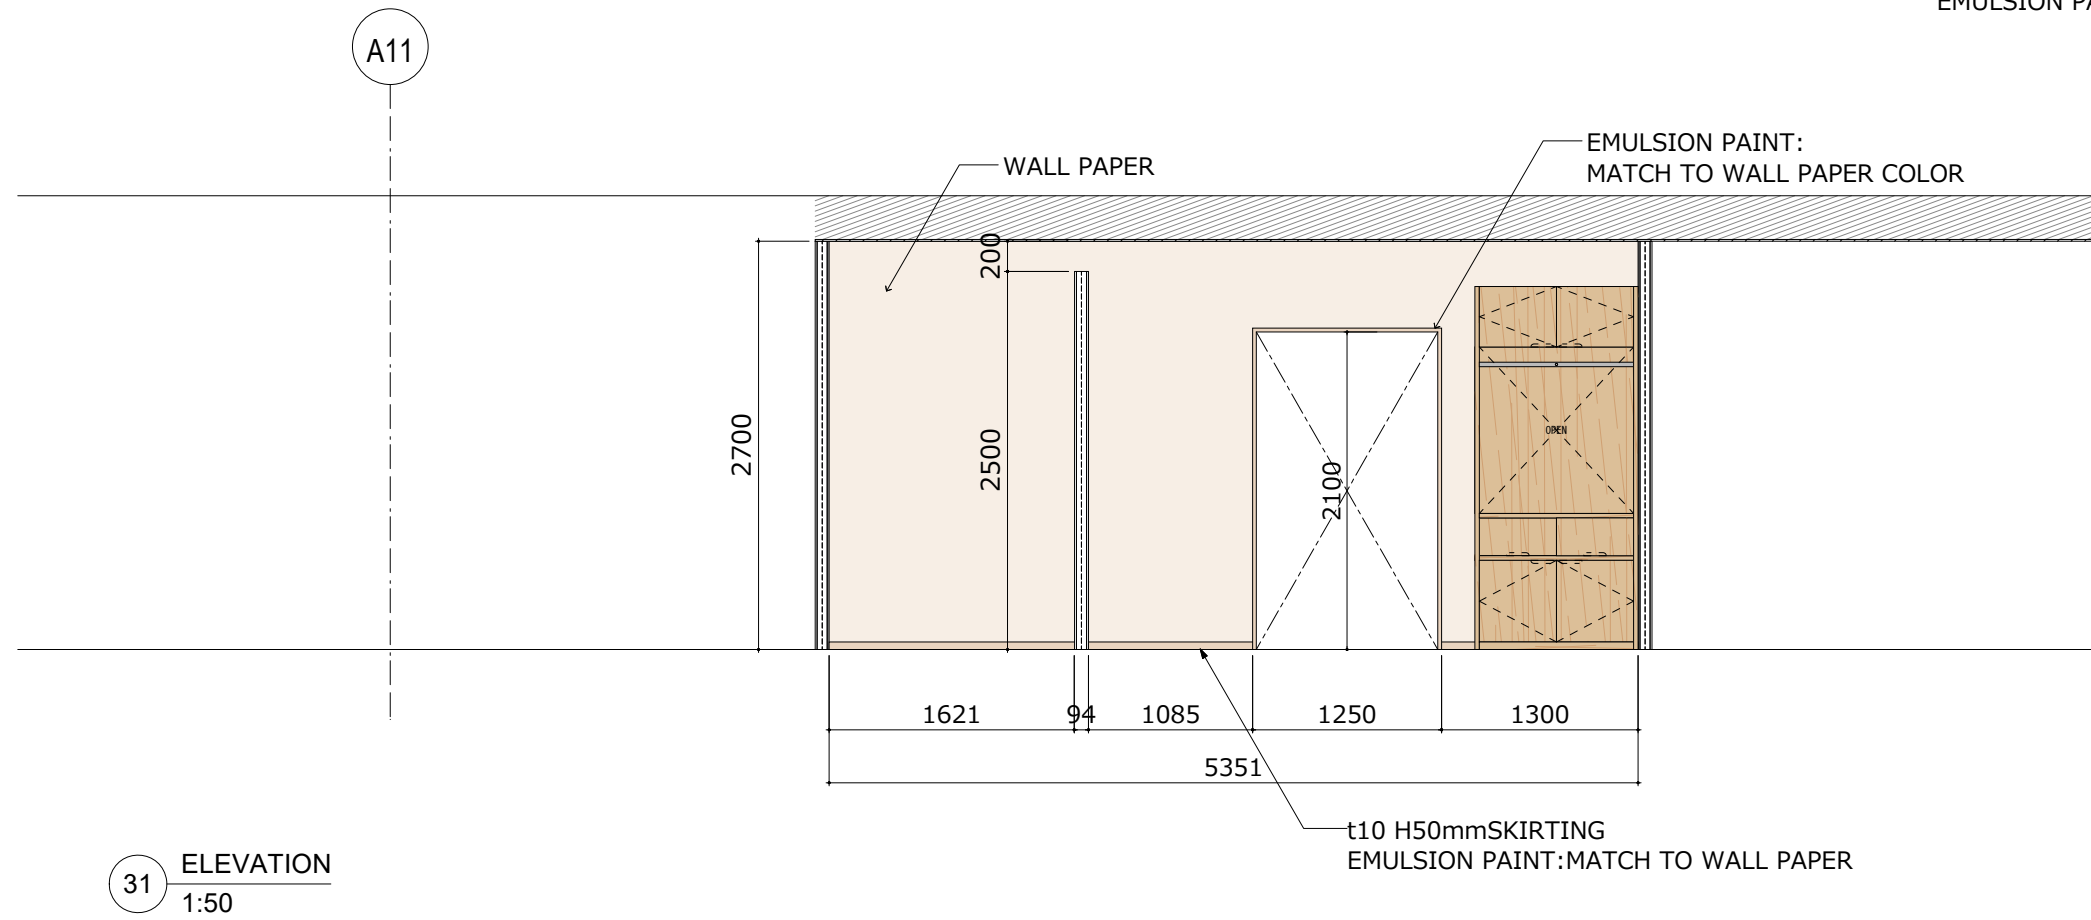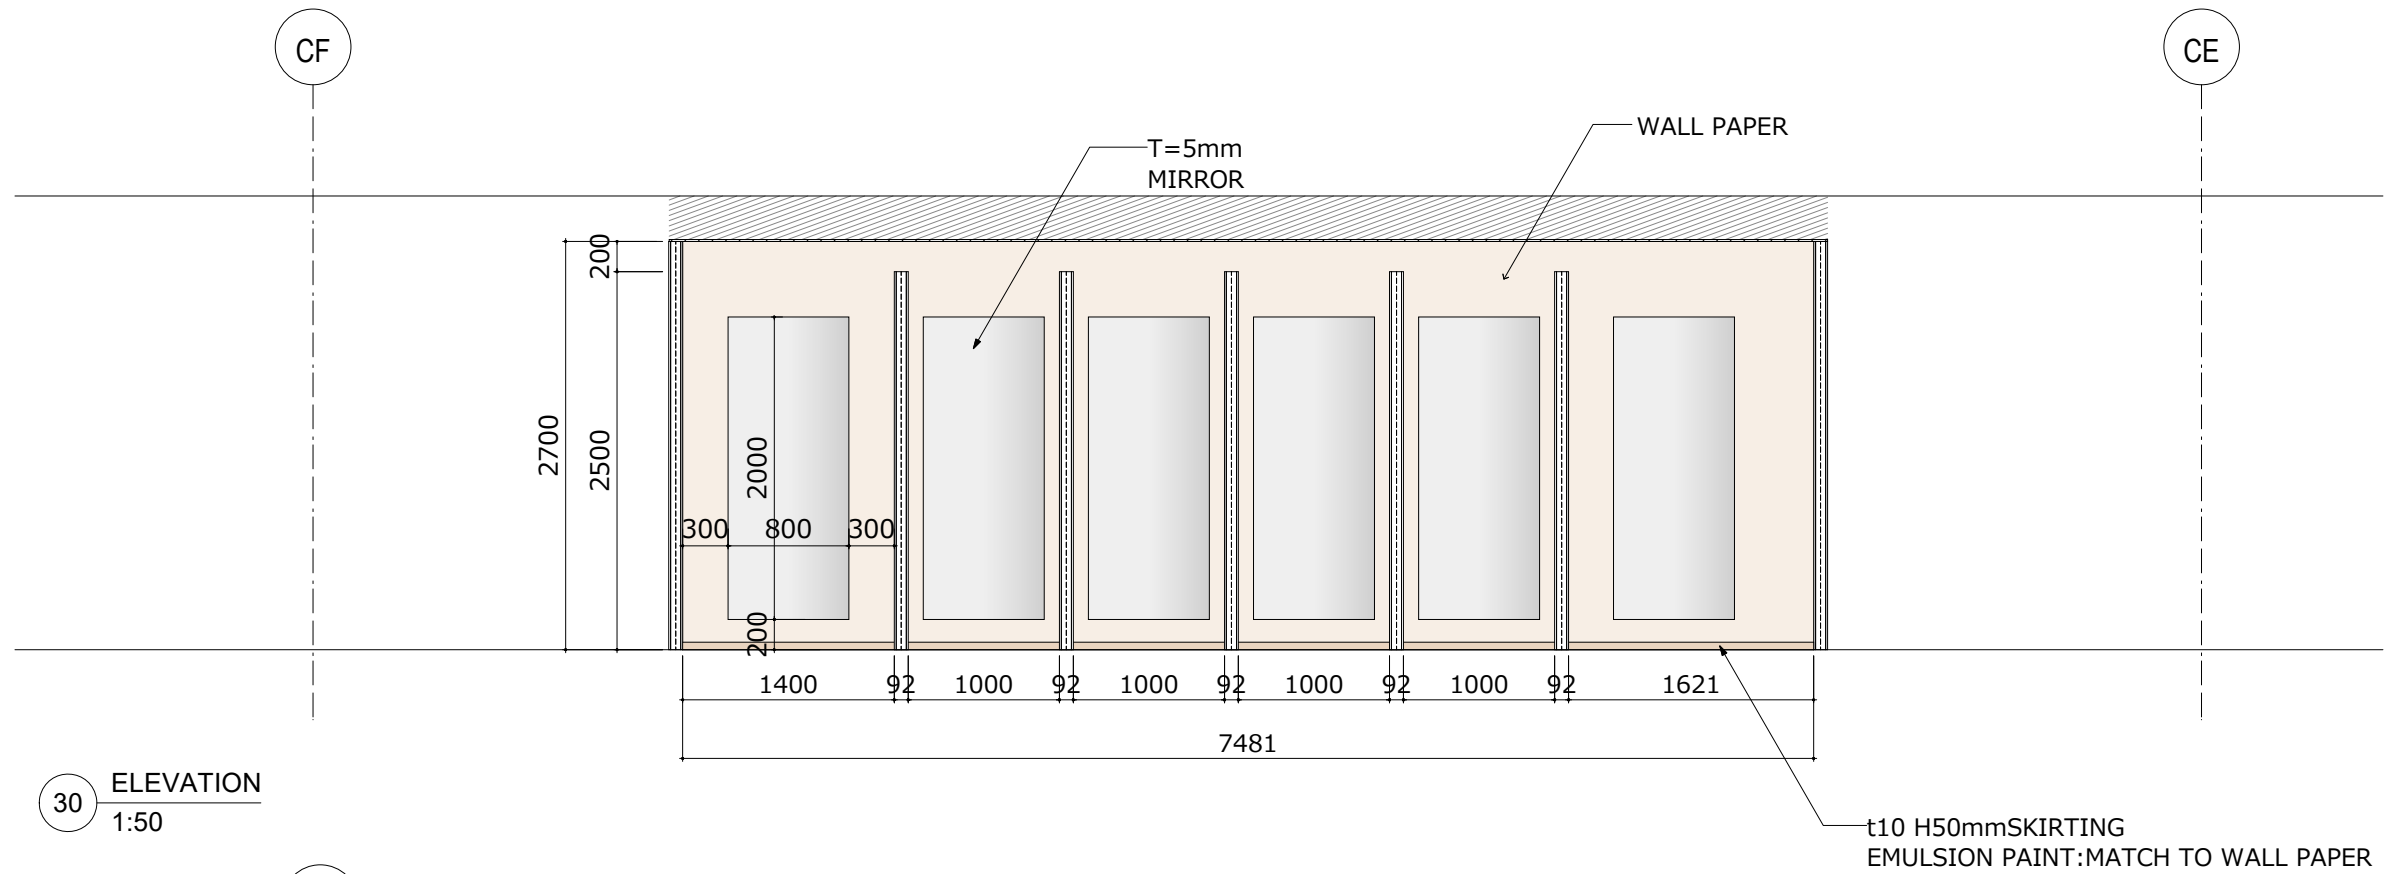


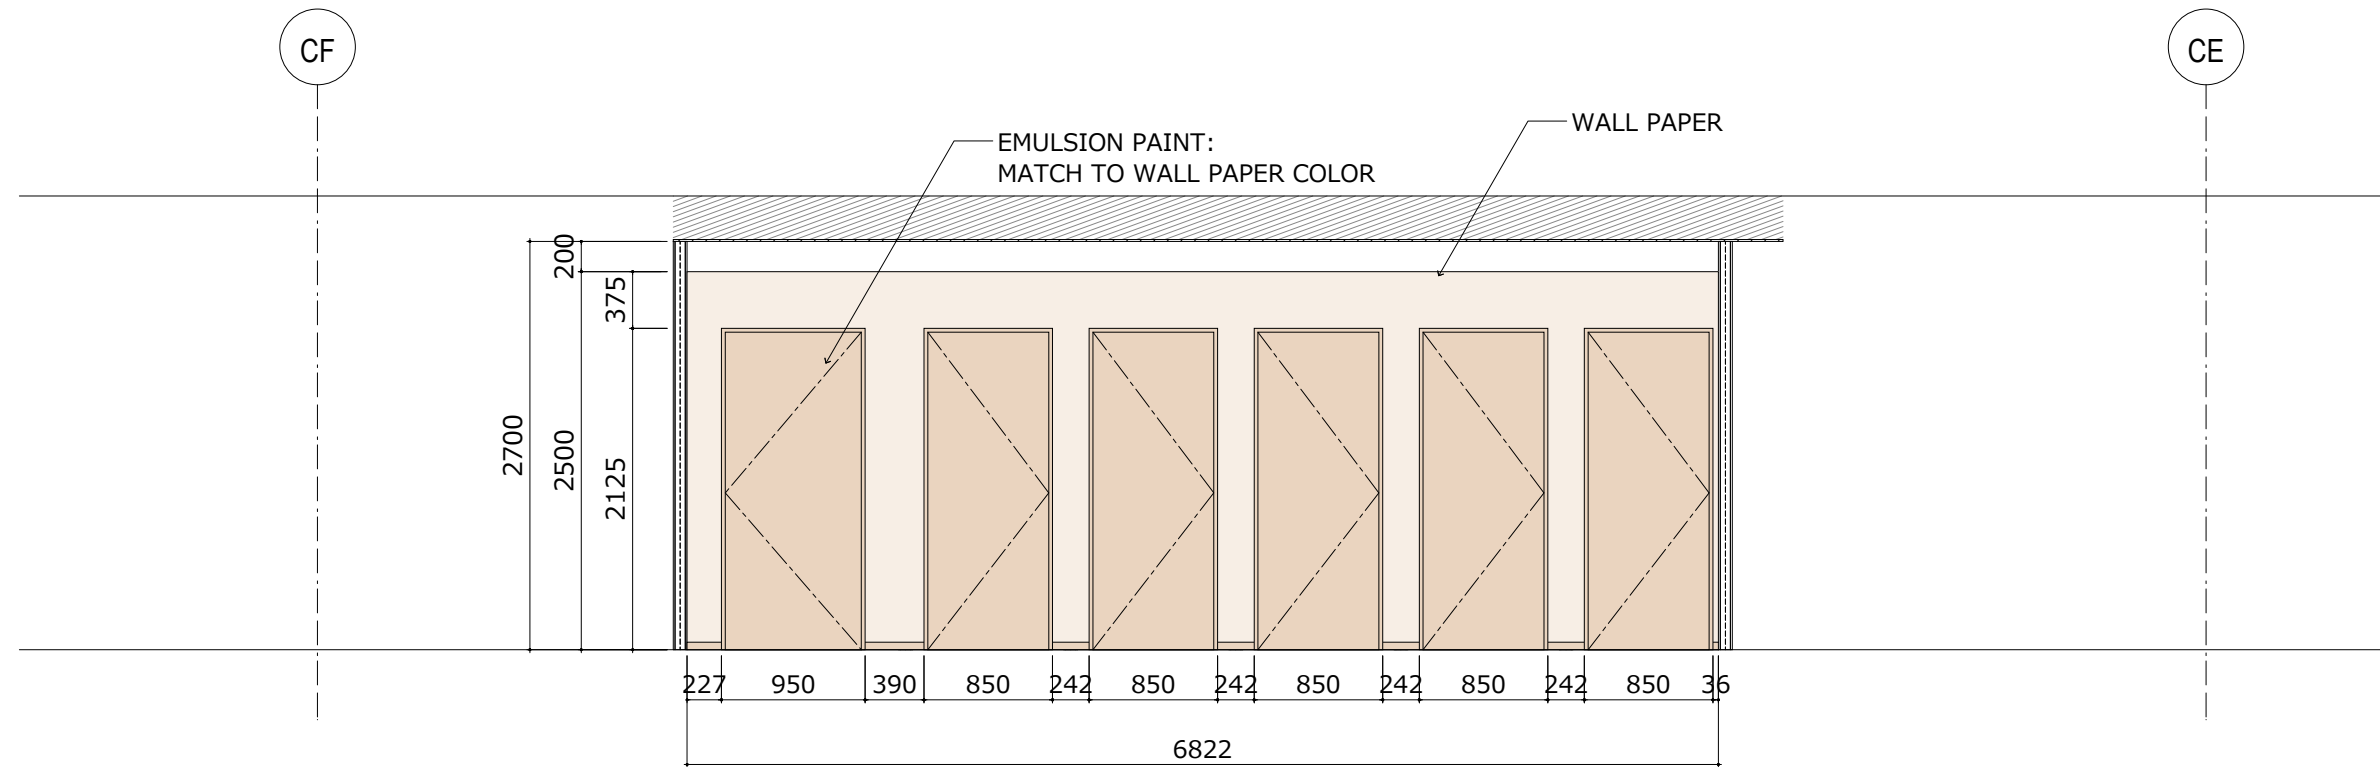

32 ELEVATION
1:50

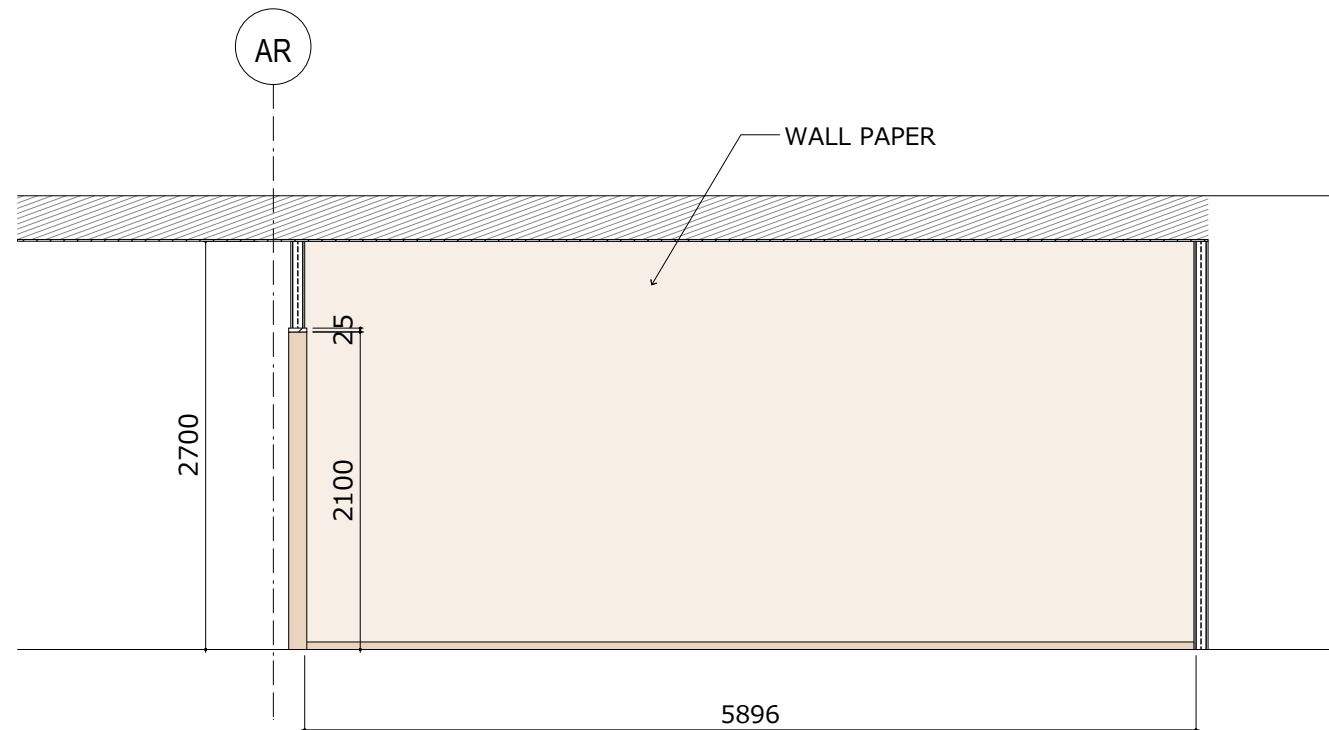

33 ELEVATION
1:50

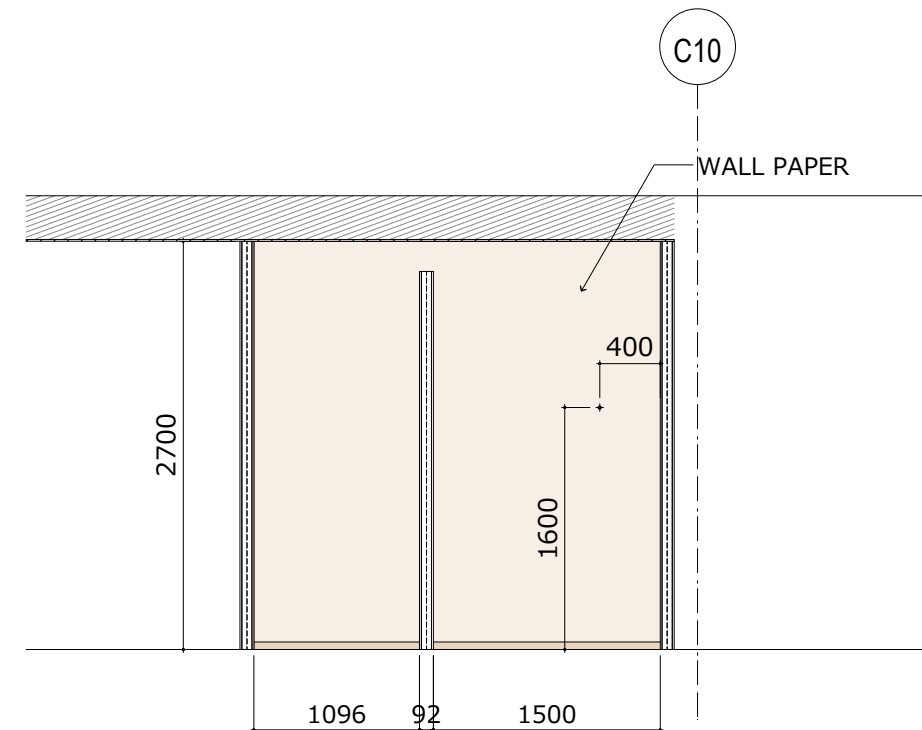

34 ELEVATION
1:50